


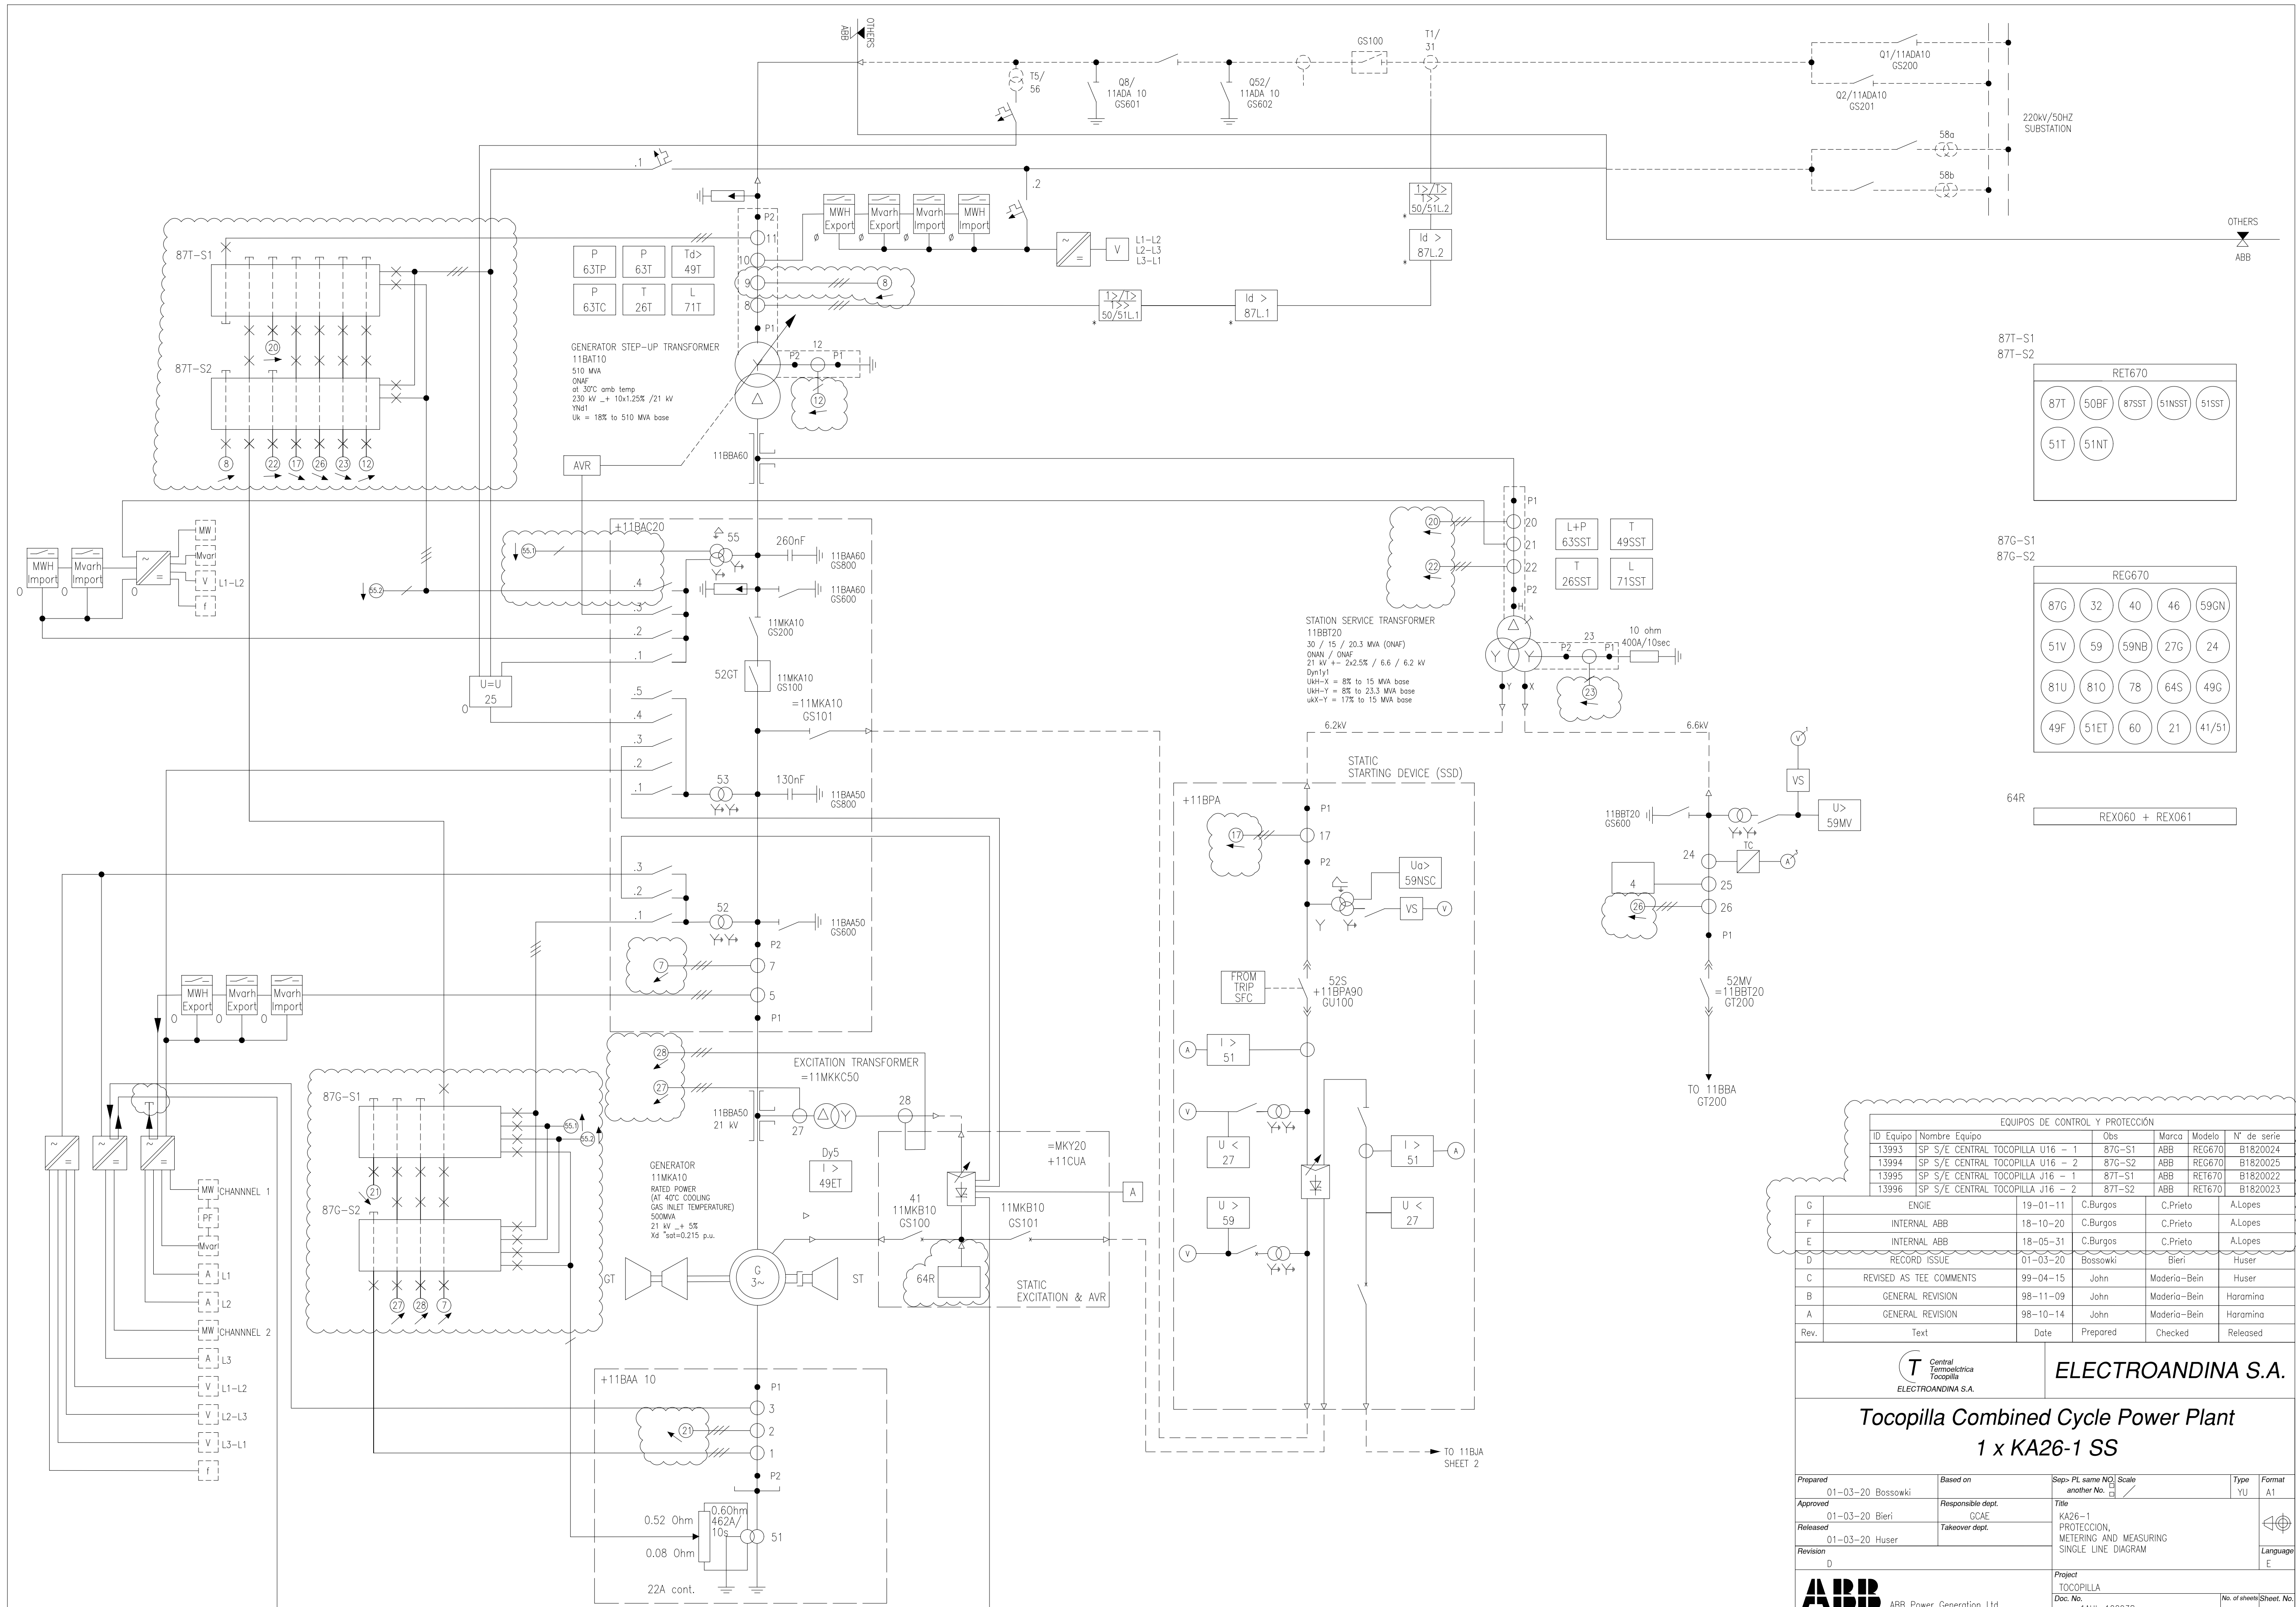

EQUIPOS DE CONTROL Y PROTECCIÓN							
ID Equipo	Nombre Equipo		Obs	Marca	Modelo	N° de serie	
13993	SP S/E CENTRAL TOCOPILLA U16	- 1	87G-S1	ABB	REC670	81820024	
13994	SP S/E CENTRAL TOCOPILLA U16	- 2	87G-S2	ABB	REC670	81820025	
13995	SP S/E CENTRAL TOCOPILLA U16	- 1	87I-S1	ABB	RET670	81820022	
13996	SP S/E CENTRAL TOCOPILLA U16	- 2	87I-S2	ABB	RET670	81820023	

G	ENGIE	19-01-11	C.Burgos	C.Prieto	A.Lopes
F	INTERNAL ABB	18-10-20	C.Burgos	C.Prieto	A.Lopes
E	INTERNAL ABB	18-05-31	C.Burgos	C.Prieto	A.Lopes
D	RECORD ISSUE	01-03-20	Bossowki	Bieri	Huser
C	REVISED AS TEE COMMENTS	99-04-15	John	Moderia-Bein	Huser
B	GENERAL REVISION	98-11-09	John	Moderia-Bein	Haramina
A	GENERAL REVISION	98-10-14	John	Moderia-Bein	Haramina
Rev.	Text	Date	Prepared	Checked	Released



Central
Termoelectrica
Tocopilla

ELECTROANDINA S.A.

ELECTROANDINA S.A.

Tocopilla Combined Cycle Power Plant

1 x KA26-1 SS

Prepared	Based on	Seпо-PL same No. Scale	Type	Format
Approved	Responsible dept.	another No. 	YU	A1
Released	Takeover dept.	Title		
Revision		KA26-1 PROTECCION, METERING AND MEASURING SINGLE LINE DIAGRAM		
D				
Project			Language	
TOCOPILLA			E	
Doc. No.			No. of sheets	
1AHL 102938			3	
			1	



ABB Power Generation Ltd