

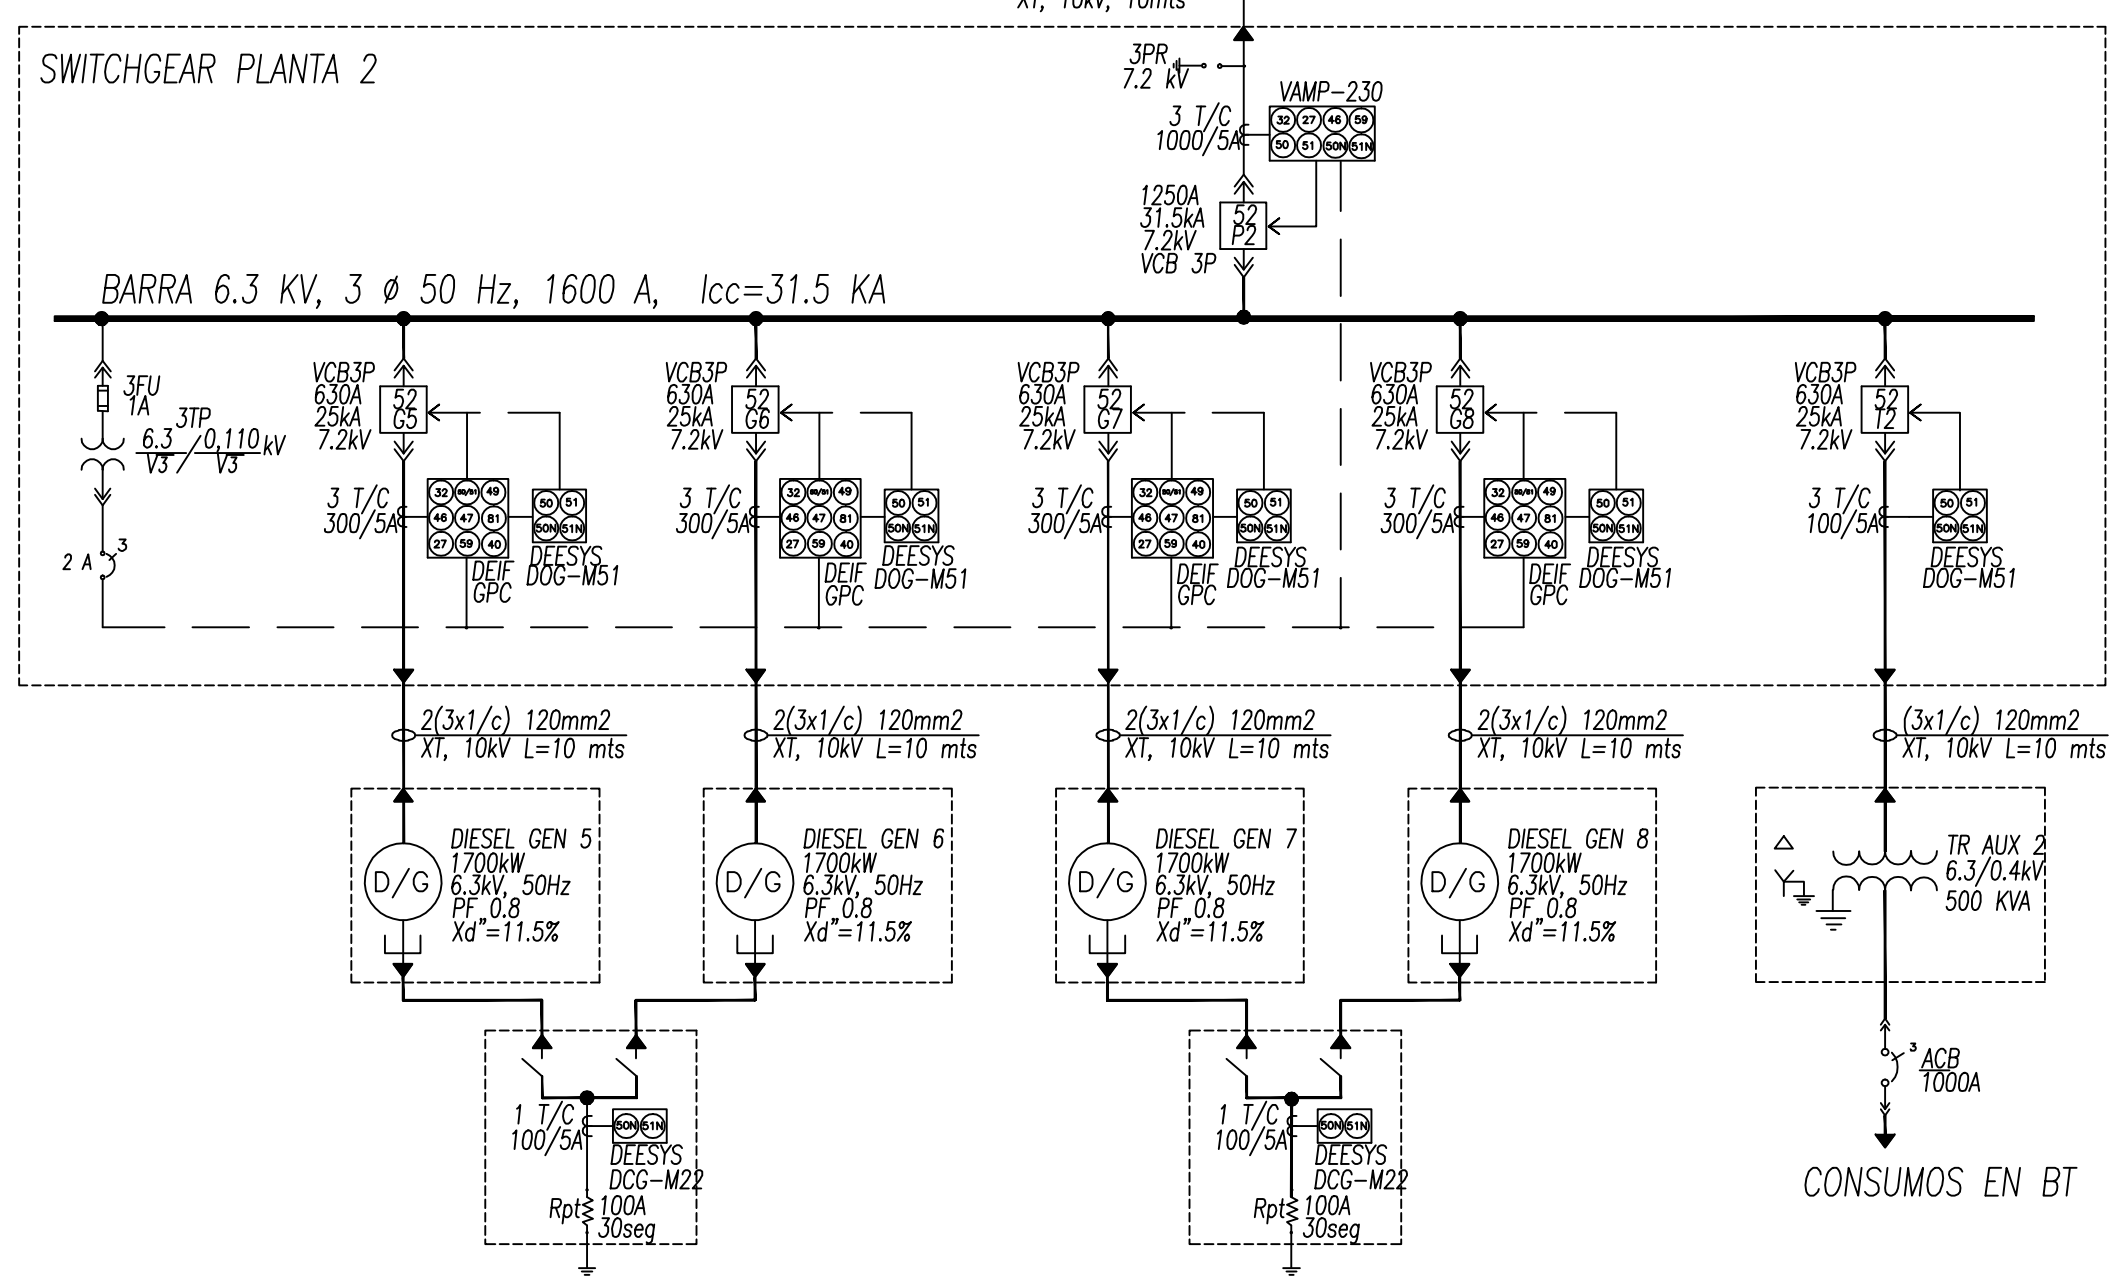
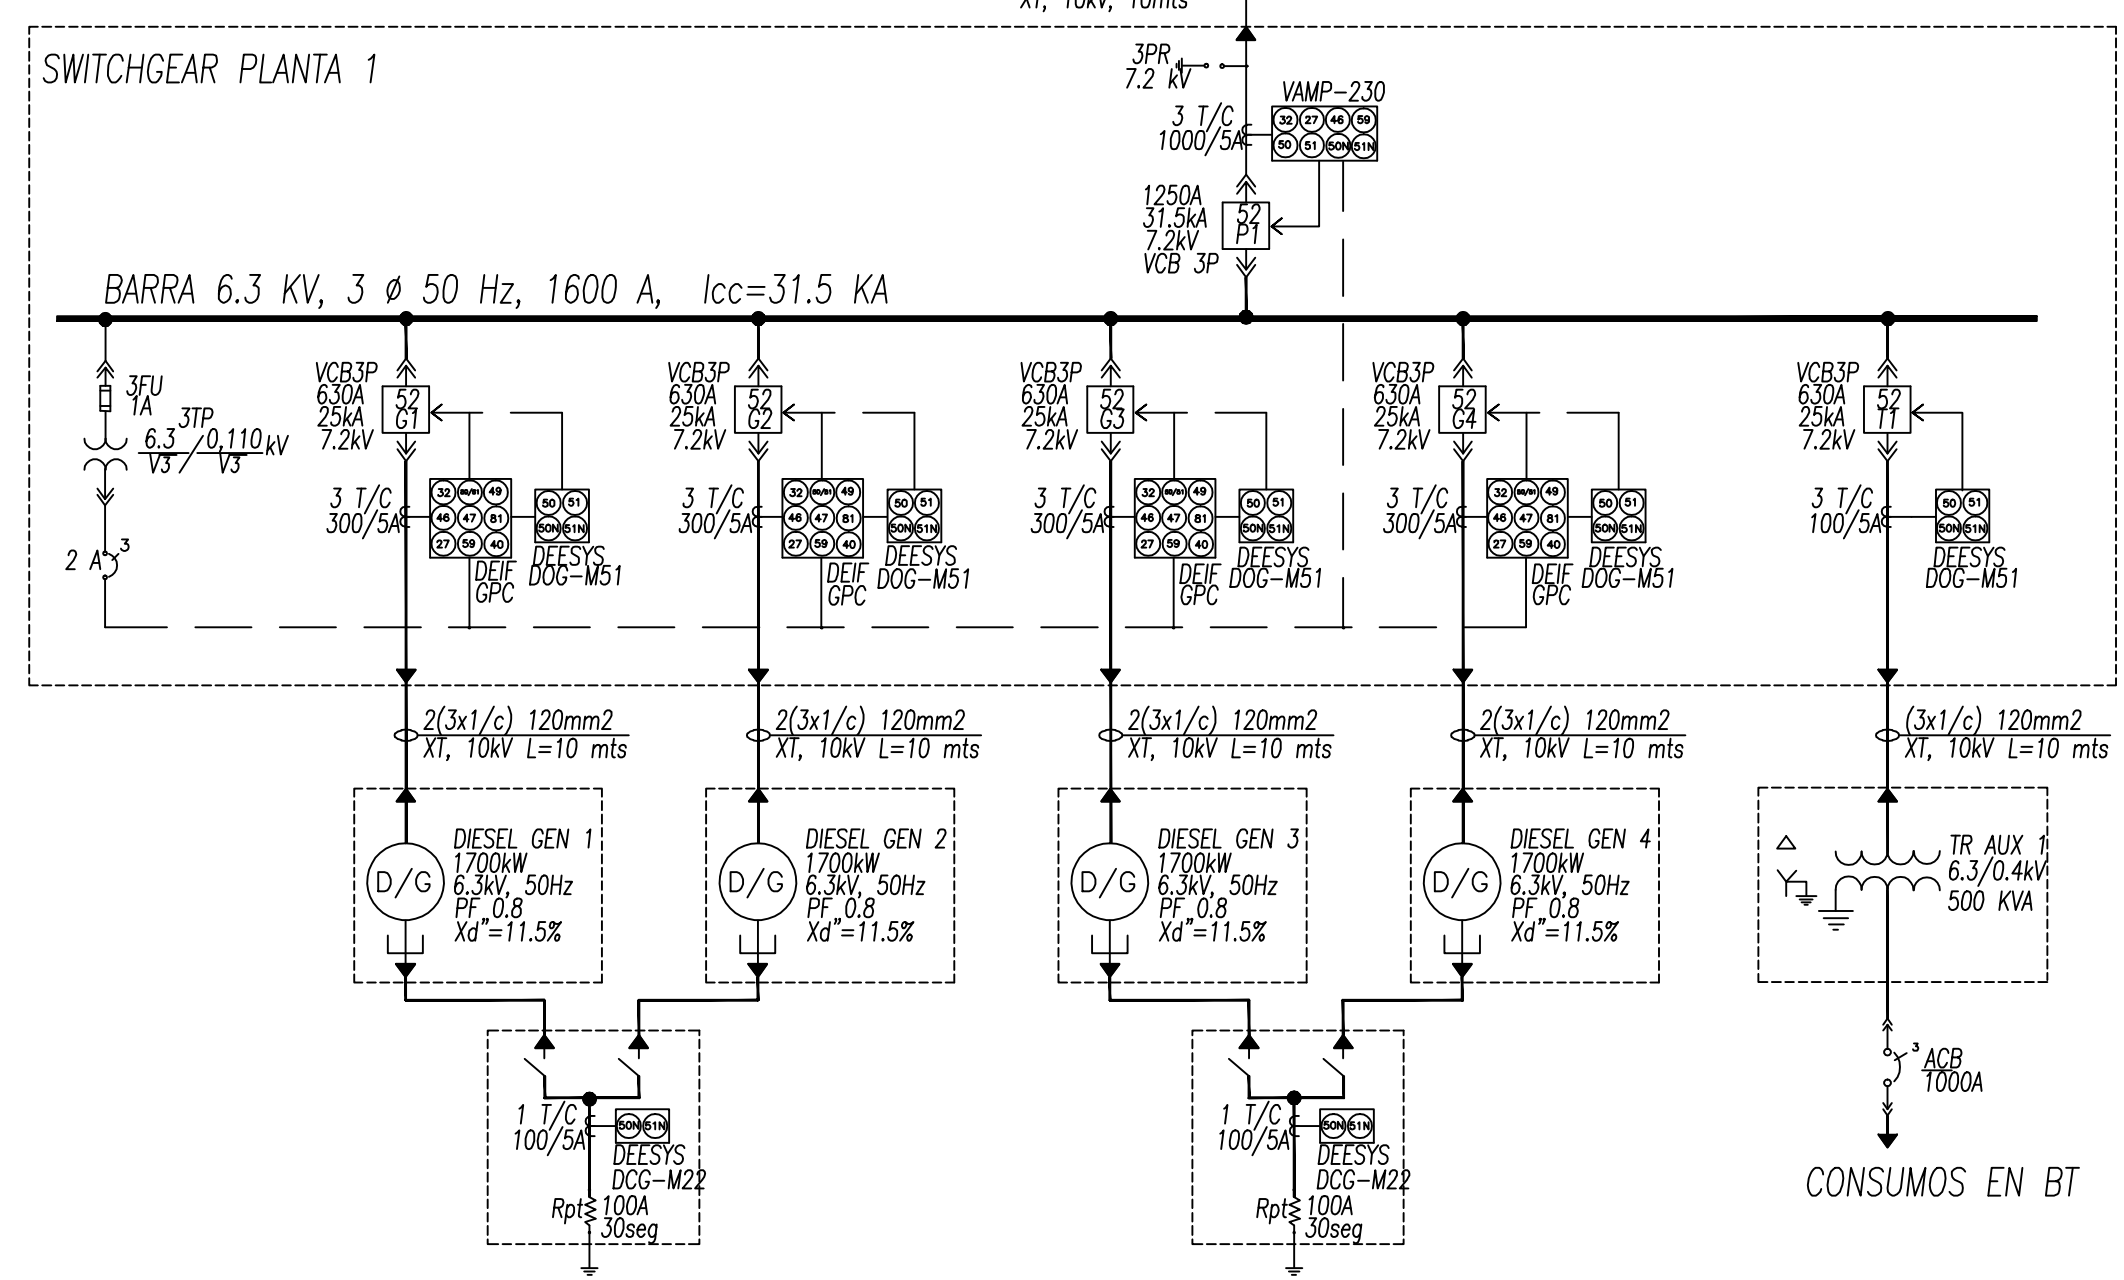
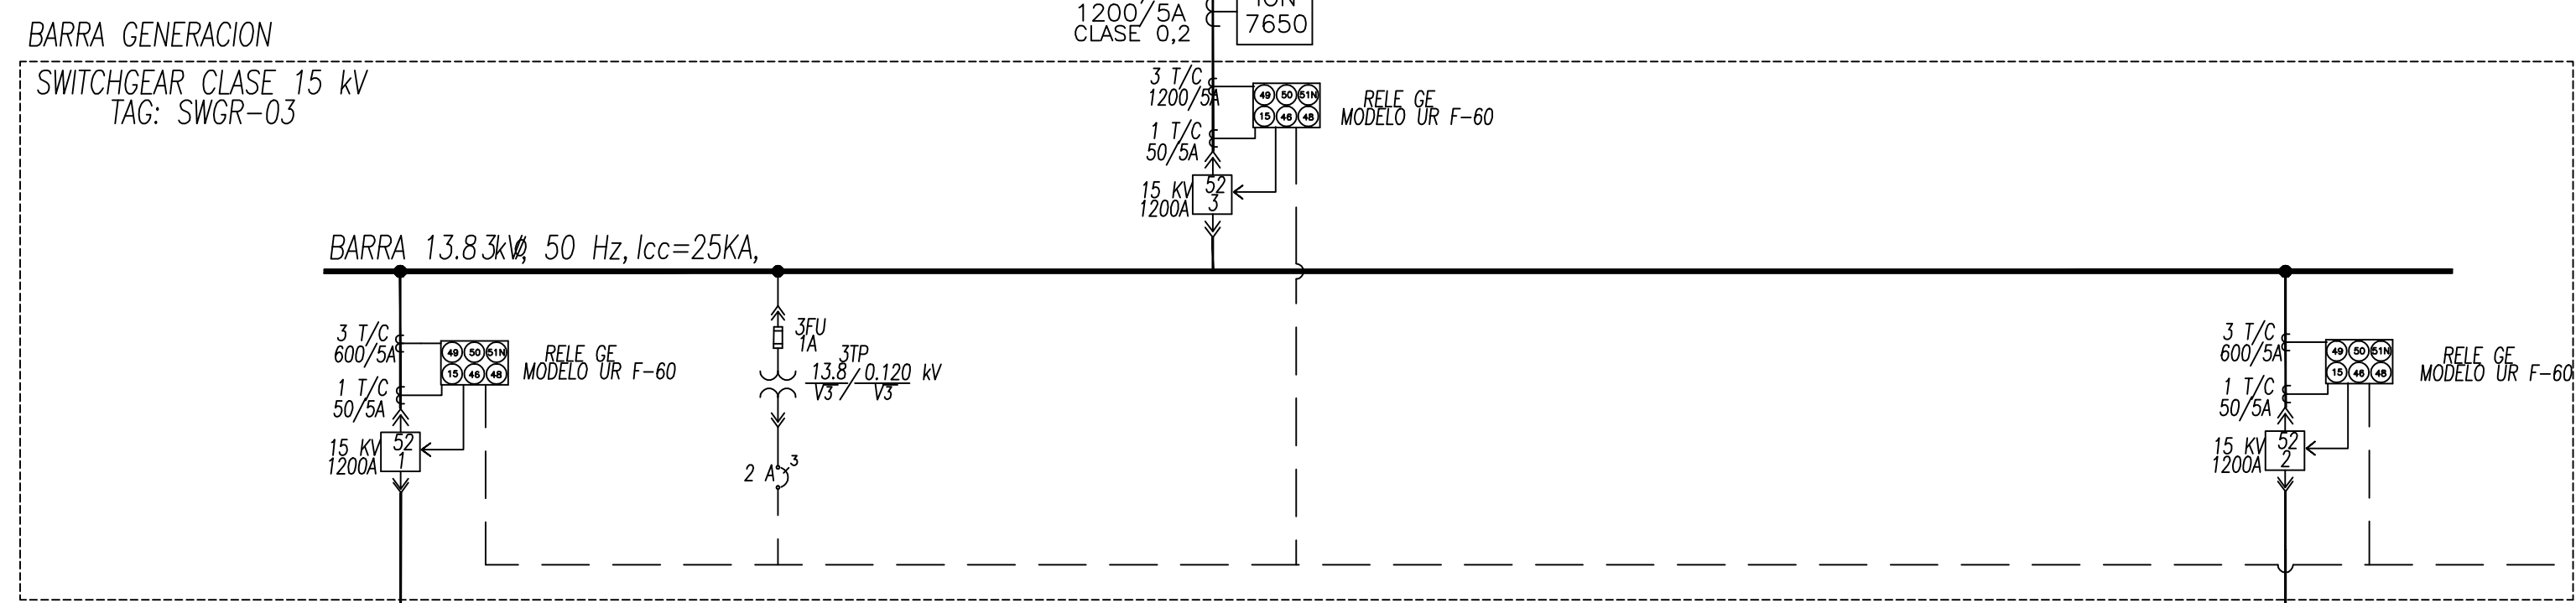


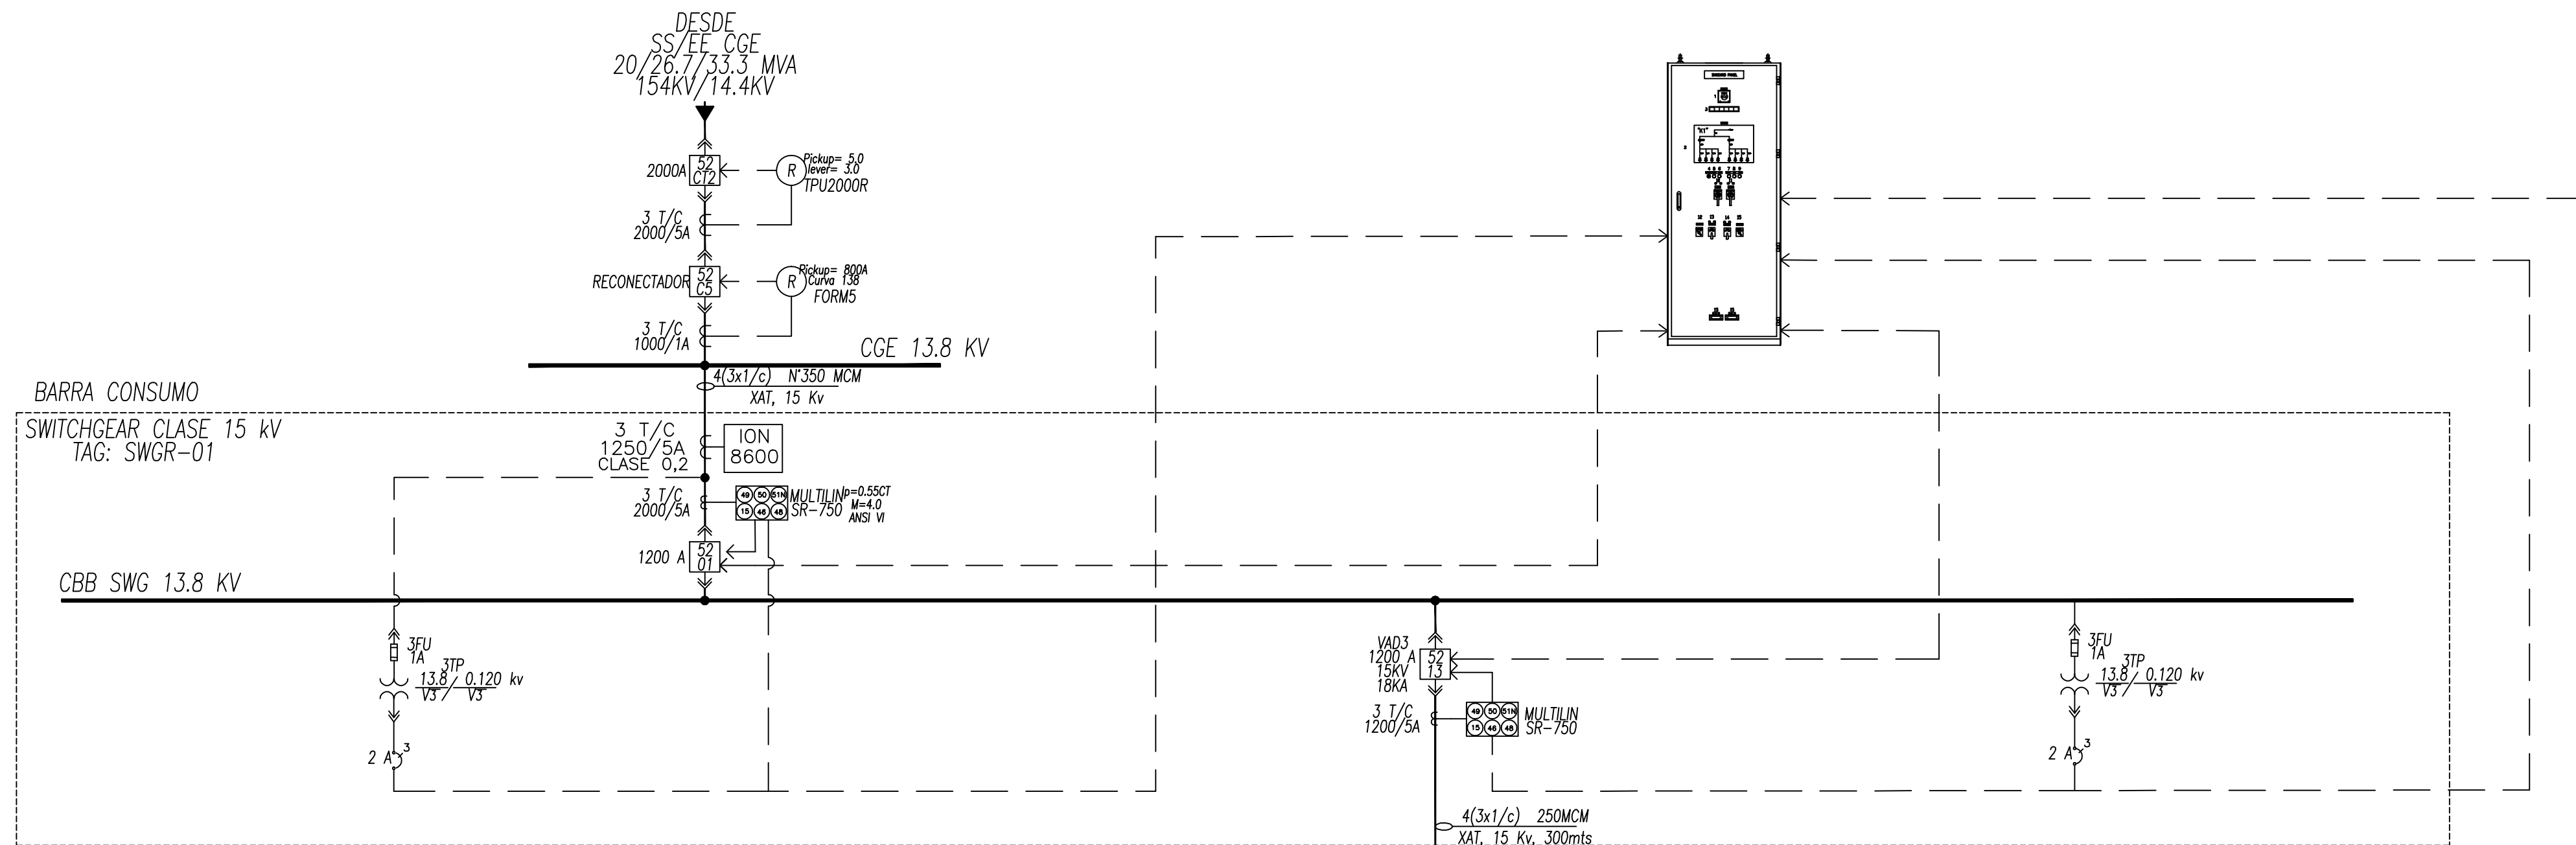

REVISIONES						PROYECTO:	
						CALCULO:	
						DIBUJO:	
						REVISO:	A.ESSMANN
						APROBO:	A.ESSMANN
						FECHA:	04-08-09
N°	FECHA	DESCRIPCION	DIBUJO	REVISO	APROBO	FECHA:	04-08-09

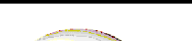

CEMENTOS BIO BIO

PROYECTO :	GRUPO DE GENERADORES		
MATERIA:	ESQUEMA DE PROTECCIONES		
ESCALA / FORMATO	PLANO N°		REV:
SIN ESCALA			A