


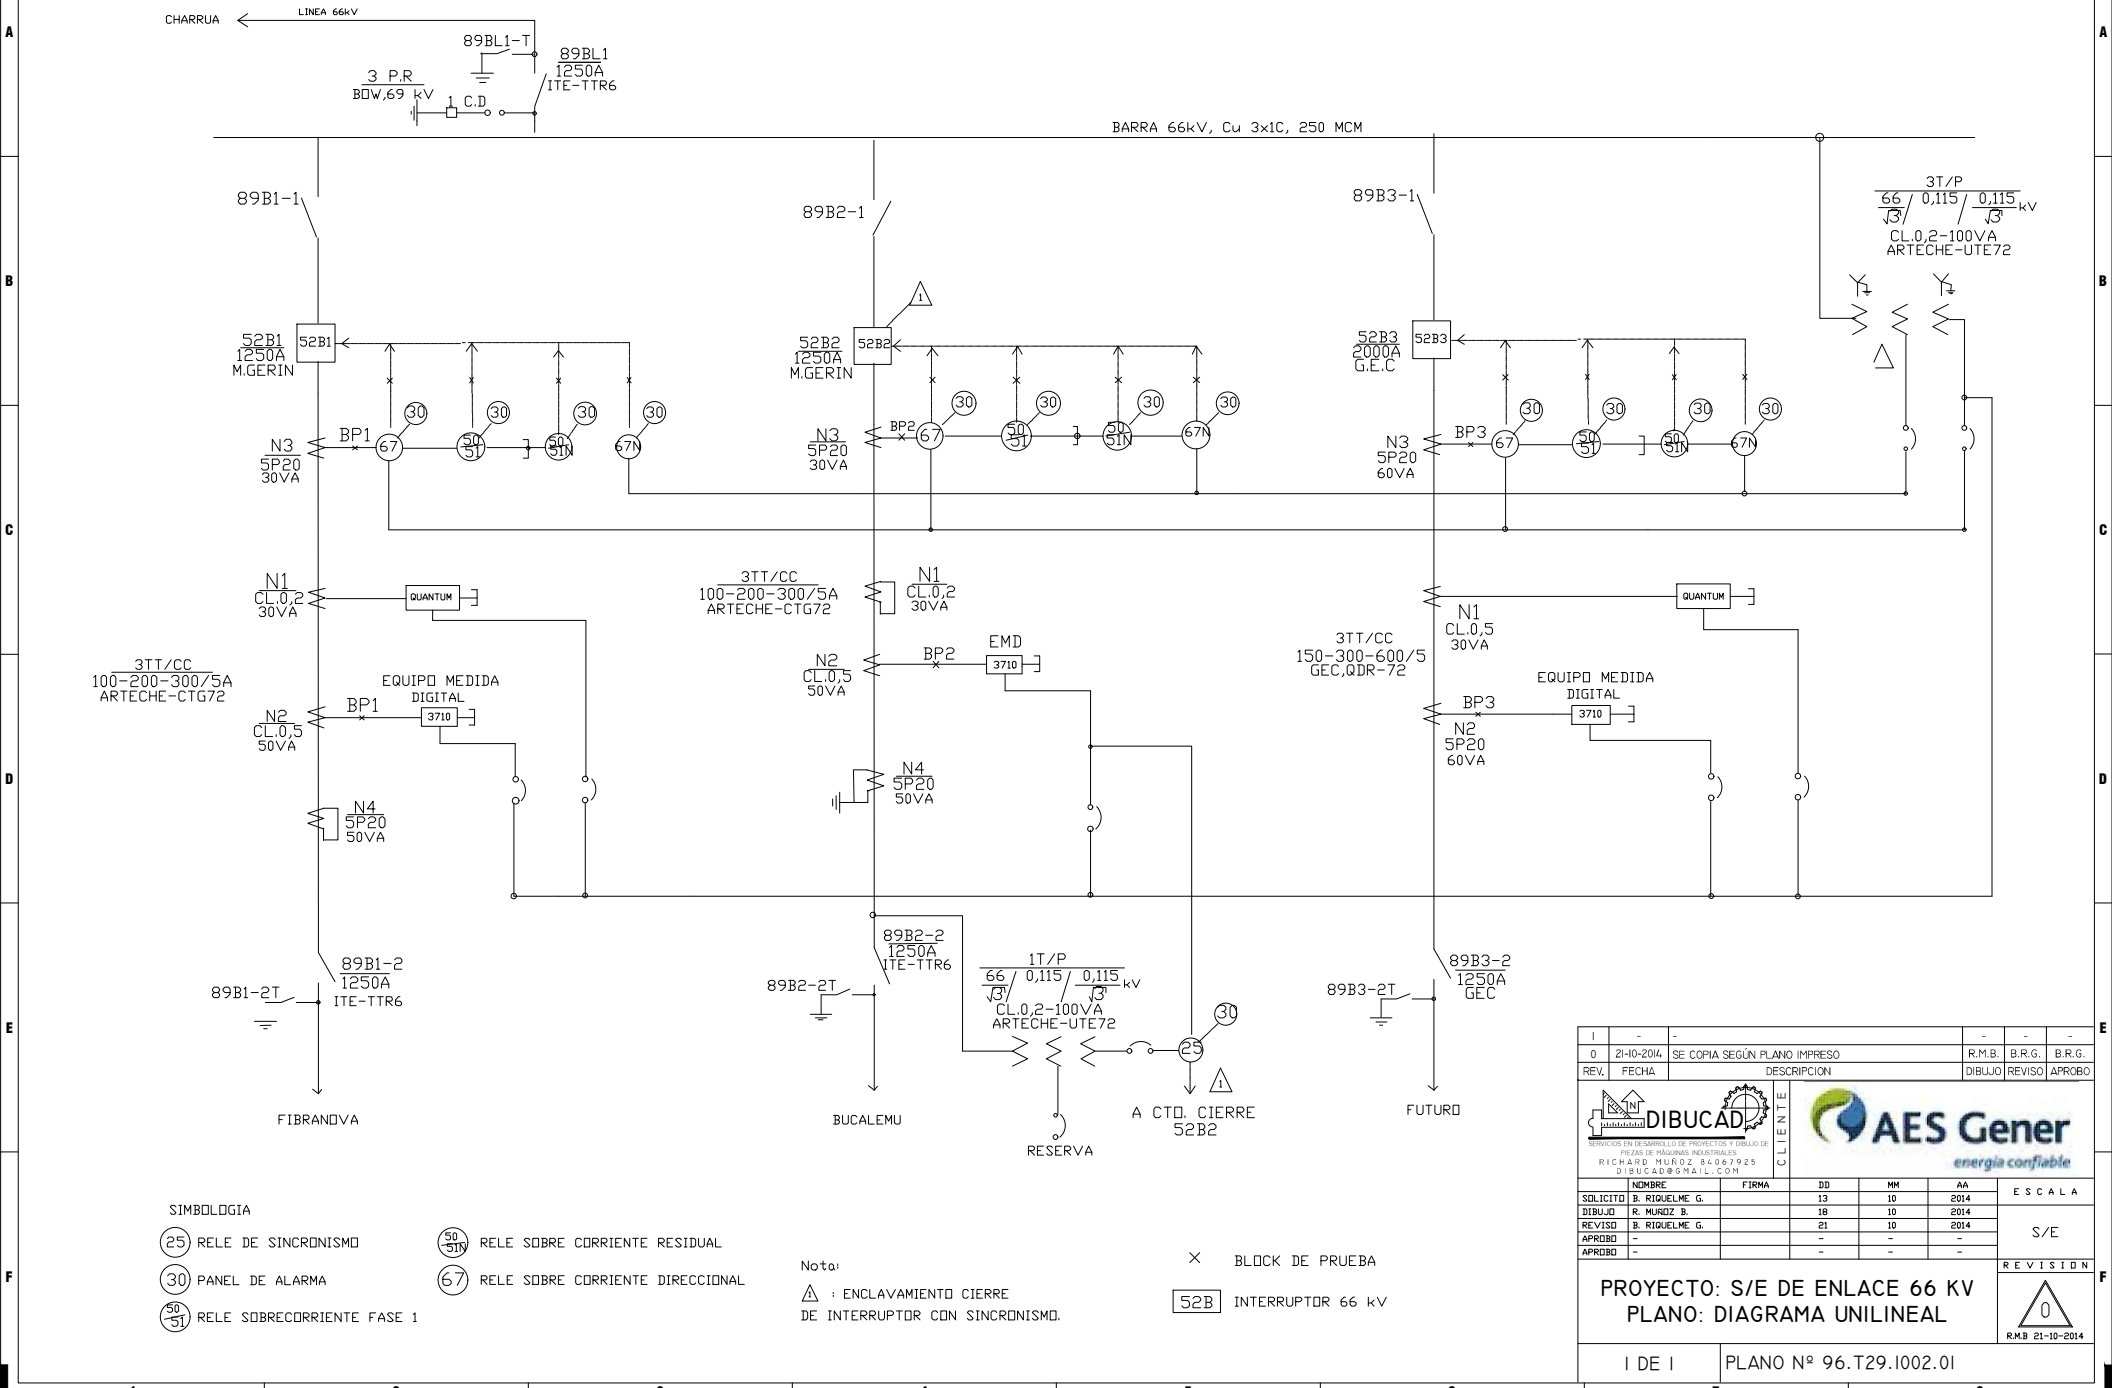

SIMBOLOGIA

- (25) RELE DE SINCRONISMO
- (30) RELE SOBRE CORRIENTE RESIDUAL
- (30) PANEL DE ALARMA
- (67) RELE SOBRE CORRIENTE DIRECCIONAL
- (50-51) RELE SOBRECORRIENTE FASE 1

Nota:
⚠ : ENCLAVAMIENTO CIERRE DE INTERRUPTOR CON SINCRONISMO.
X BLOCK DE PRUEBA
52B INTERRUPTOR 66 kV

1	-	-	-	-	-
0	24-10-2014	SE COPIA SEGUN PLANO IMPRESO	R.M.B.	B.R.G.	B.R.G.
REV.	FECHA	DESCRIPCION	DIBUJO	REVISO	APROBO

NOMBRE	FIRMA	DD	MM	AA
SOLICITO B. RIQUELME G.		13	10	2014
DIBUJO R. MUÑOZ B.		18	10	2014
REVISO B. RIQUELME G.		21	10	2014
APROBO -		-	-	-
APROBO -		-	-	-

ESCALA	REVISION
S/E	0

PROYECTO: S/E DE ENLACE 66 KV
PLANO: DIAGRAMA UNILINEAL
I DE I PLANO N° 96.T29.1002.01