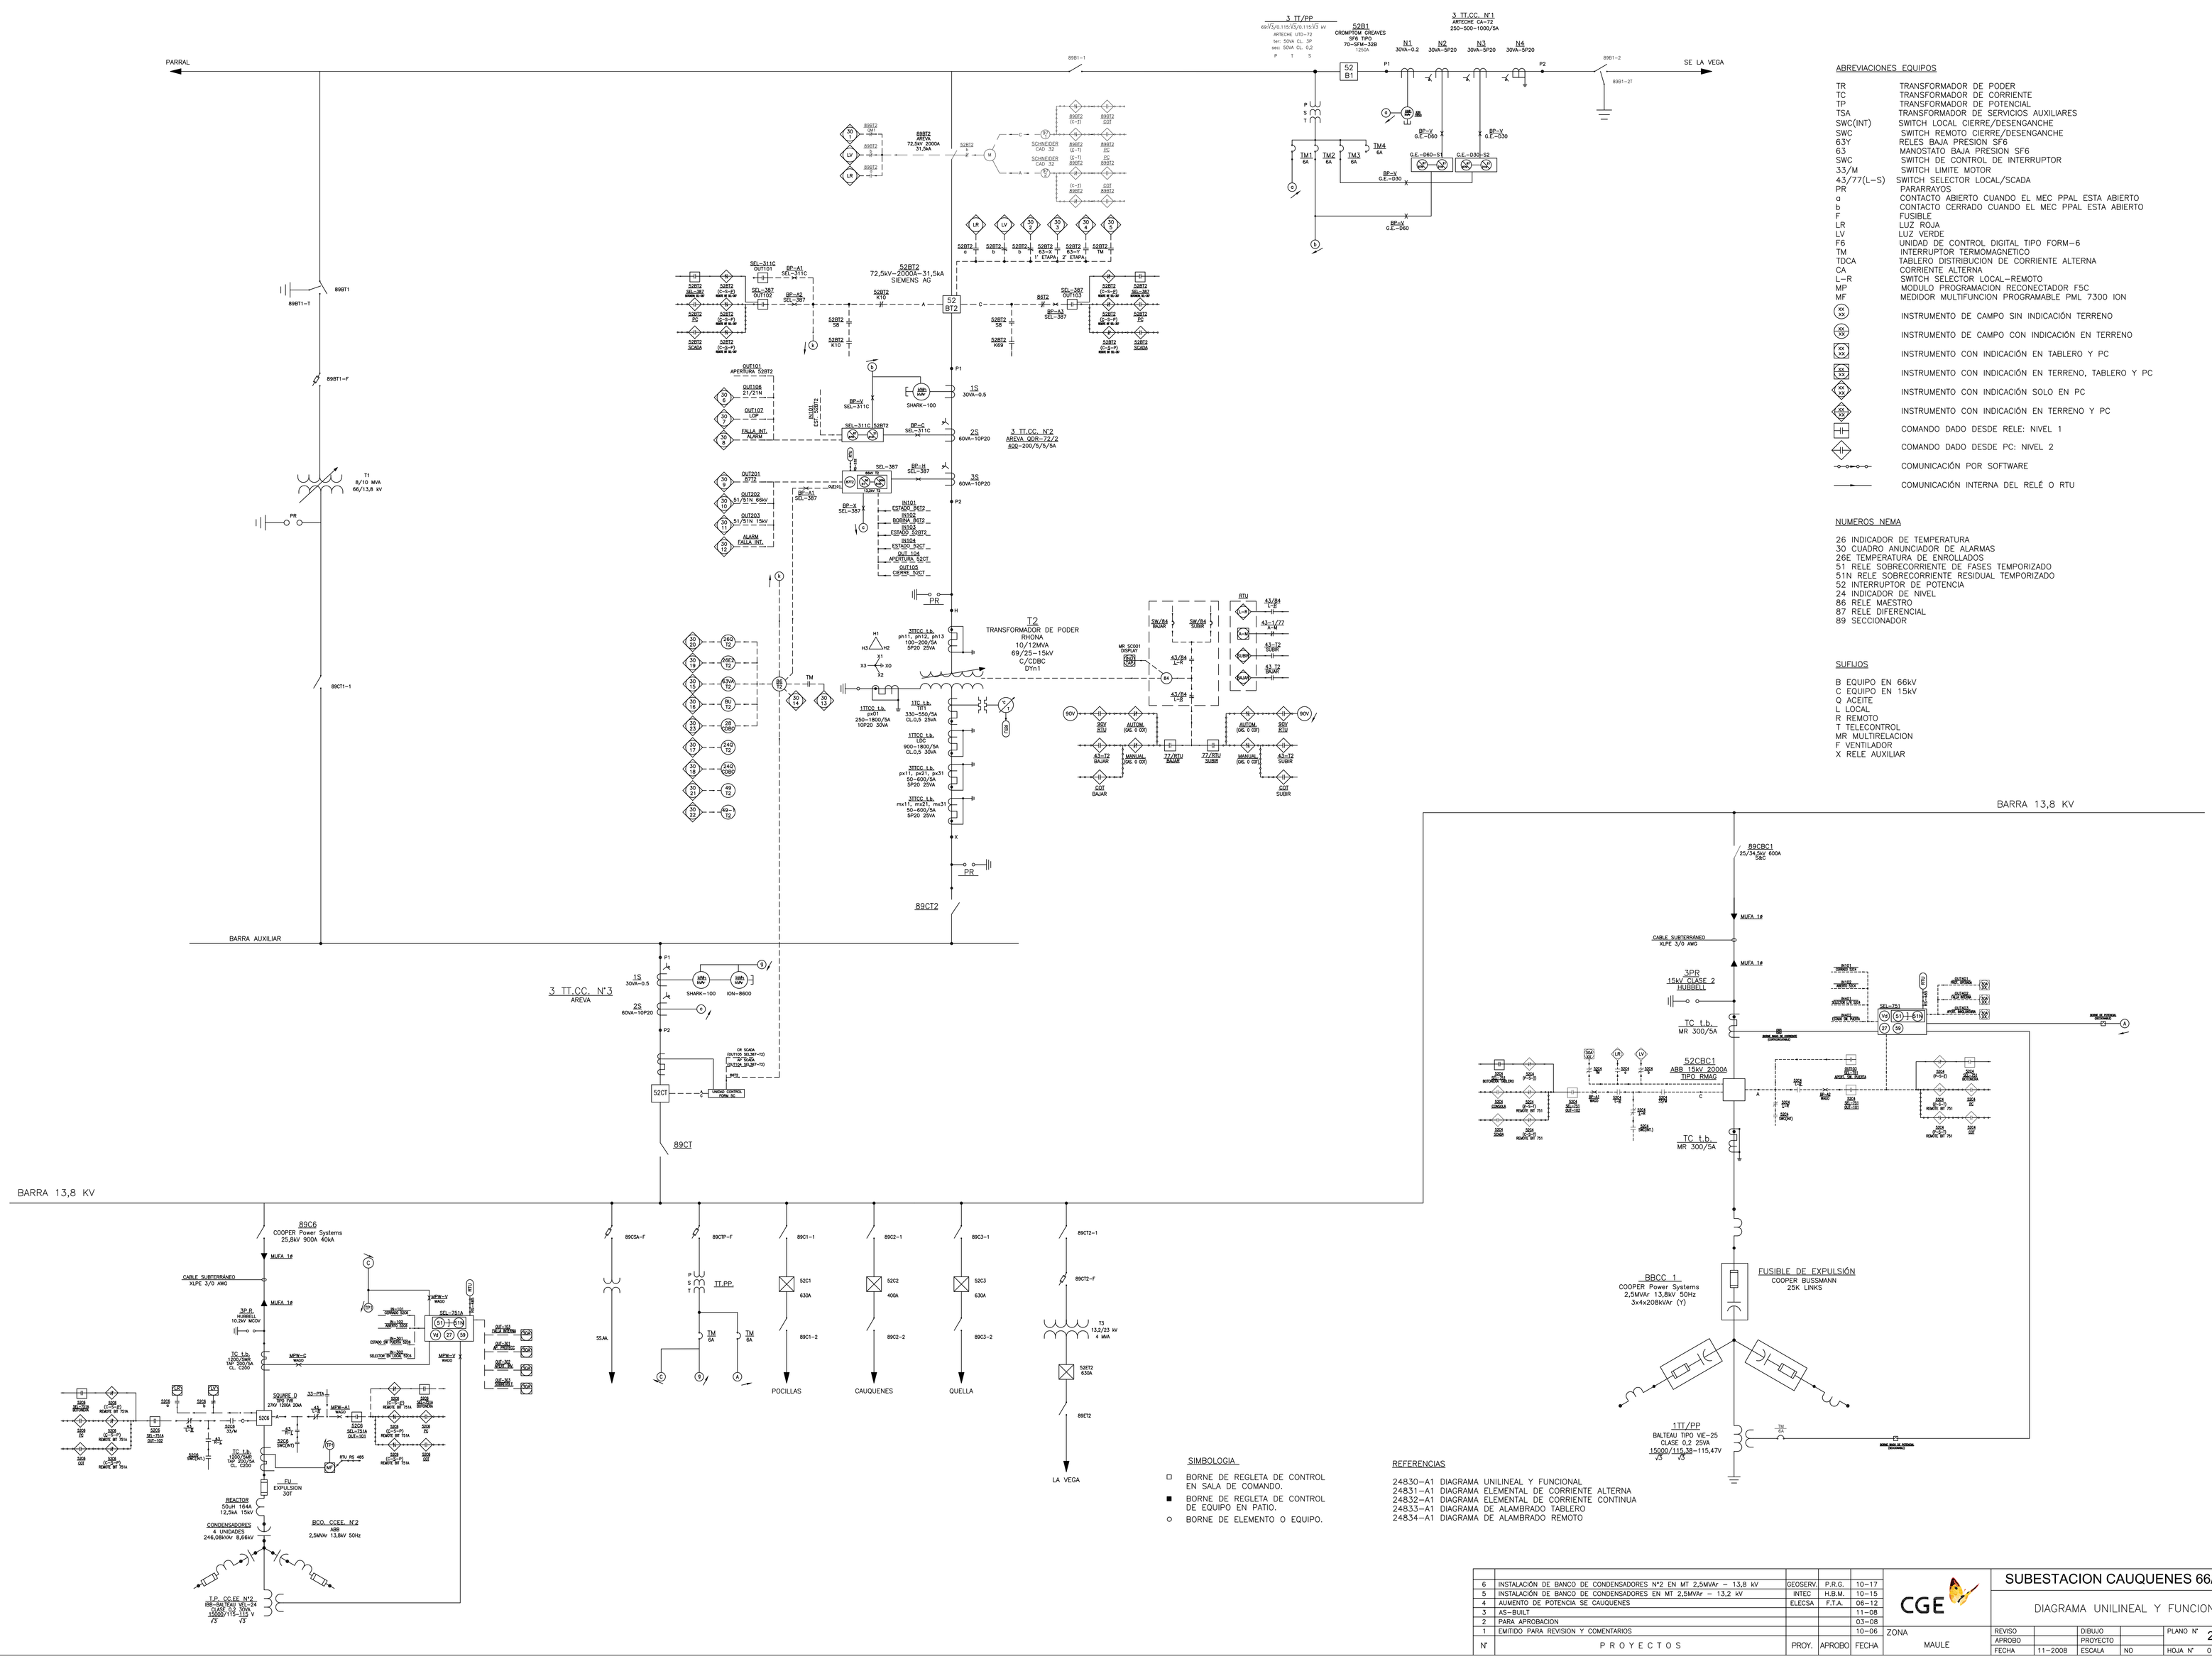


Nº	PROYECTOS	PROY.	APROBO	FECHA
6	INSTALACIÓN DE BANCO DE CONDENSADORES N°2 EN MT 2,5MVAr – 13,8 kV	GEOSERV	P.R.G.	10–17
5	INSTALACIÓN DE BANCO DE CONDENSADORES EN MT 2,5MVAr – 13,2 kV	INTEC	H.B.M.	10–15
4	AUMENTO DE POTENCIA SE CAUQUENES	ELECSA	F.T.A.	06–12
3	AS–BUILT			11–08
2	PARA APROBACION			03–08
1	EMITIDO PARA REVISION Y COMENTARIOS			10–06

ZONA: MAULE

CGE

SUBESTACION CAUQUENES 66/13,8kV

DIAGRAMA UNILINEAL Y FUNCIONAL

REVISO		DIBUJO		PLANO Nº	24830-A0
APROBO		PROYECTO			
FECHA	11–2008	ESCALA	NO	HOJA Nº	01 SIGUE EN 02