



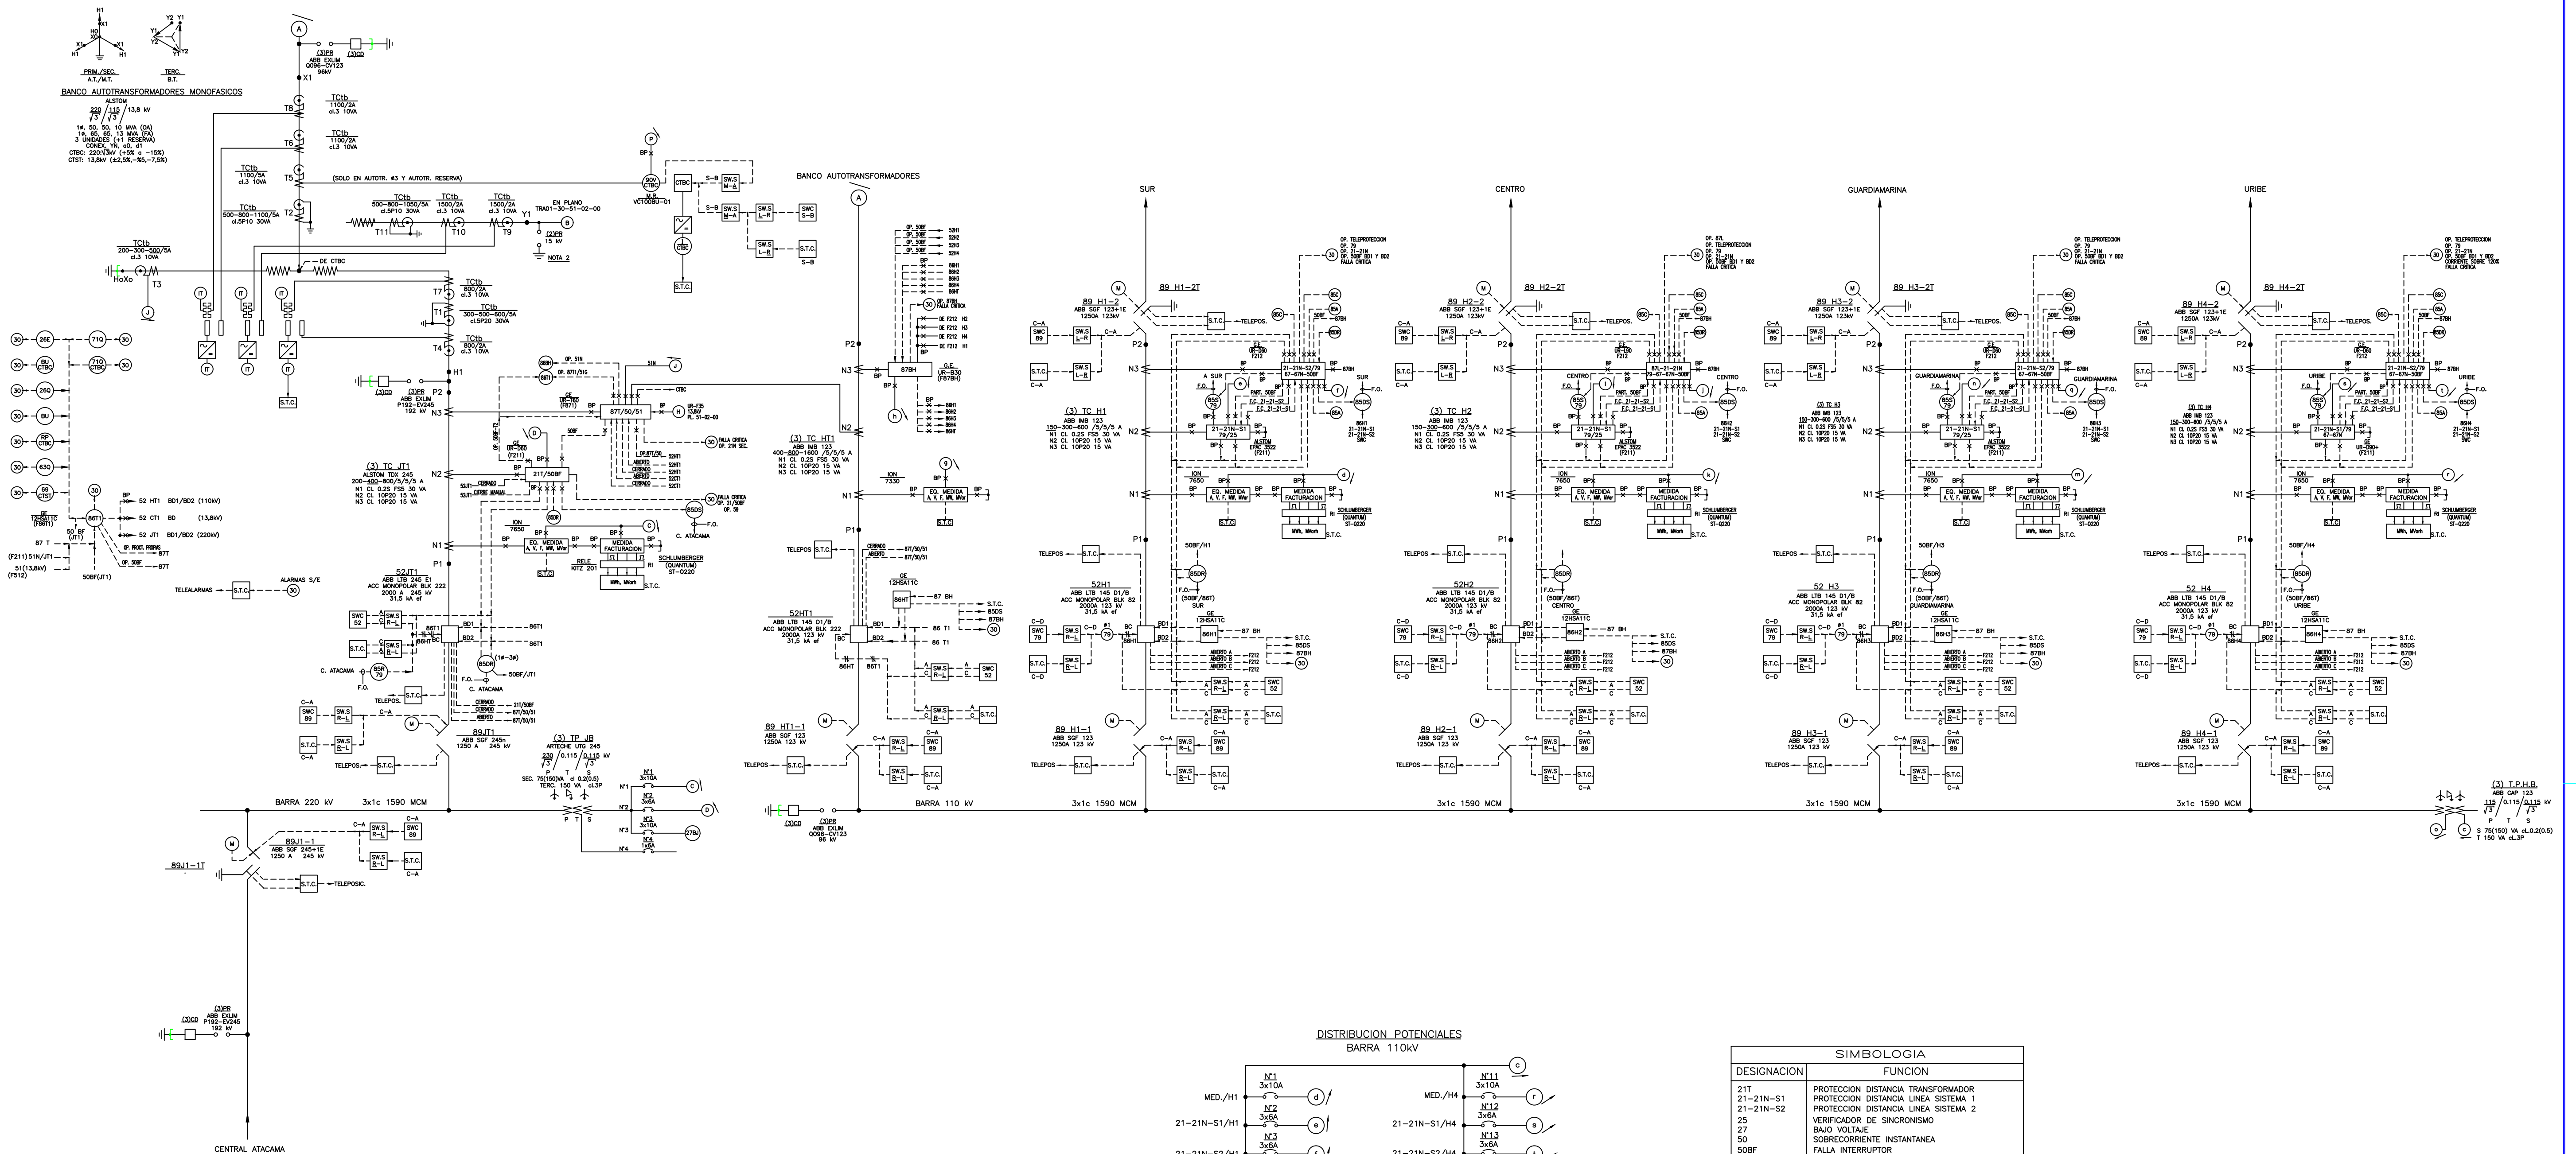

DISTRIBUCION POTENCIALES  
BARRA 110kV

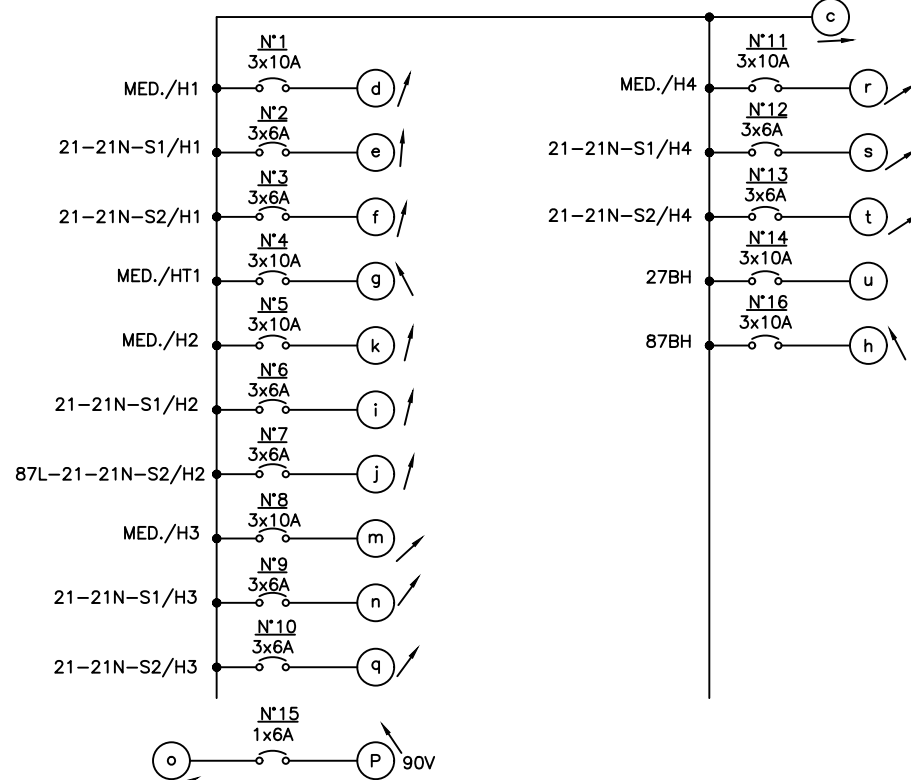

| SIMBOLOGIA  |                                           |
|-------------|-------------------------------------------|
| DESIGNACION | FUNCION                                   |
| 21T         | PROTECCION DISTANCIA TRANSFORMADOR        |
| 21-21N-S1   | PROTECCION DISTANCIA LINEA SISTEMA 1      |
| 21-21N-S2   | PROTECCION DISTANCIA LINEA SISTEMA 2      |
| 25          | VERIFICADOR DE SINCRONISMO                |
| 27          | BAJO VOLTAJE                              |
| 50          | SOBRECORRIENTE INSTANTANEA                |
| 50BF        | FALLA INTERRUPTOR                         |
| 51          | SOBRECORRIENTE FASES                      |
| 51N         | SOBRECORRIENTE RESIDUAL                   |
| 67          | PROT. SOBRECORRIENTE DIRECCIONAL FASES    |
| 67N         | PROT. SOBRECORRIENTE DIRECCIONAL TIERRA   |
| 710         | BAJO NIVEL ACEITE                         |
| 79          | RECONEXION                                |
| 85A         | ACELERACION PROT. DIST. (REC/EMIS)        |
| 85C         | COMPARACION DIRECC. (REC/EMIS)            |
| 85DR        | RECEPCION DESENGANCHE DIRECTO             |
| 85DS        | TRANSMISION DESENGANCHE DIRECTO           |
| 85R/79      | RECEPCION ORDEN RECONEXION                |
| 86T1        | RELE AUX. PROT. DIF. TRANSF.              |
| 86H         | RELE AUX. PROT. DIF. BARRAS 110kV         |
| 87BH        | PROTECC. DIFERENCIAL BARRAS 110kV         |
| 87T         | PROTECC. DIFERENCIAL TRANSF.              |
| 90V         | REGULADOR VOLT.                           |
| BP          | BLOQUE DE PRUEBA                          |
| CTBC        | CAMBIADOR TOMAS BAJO CARGA                |
| CTST        | CAMBIADOR TOMAS SIN TENSION               |
| S.T.C.      | SISTEMA TERMINAL DE CONTROL               |
| I/CTBC      | INDICADOR POSICION CAMB. TOMAS BAJO CARGA |
| BU          | BUCHHOLZ                                  |

NOTA:  
1.- LOS NUCLEOS N2 Y N3 DE LOS TC. J11, H1, H2, H3  
Y H4 DEBEN TENER CARACTERISTICA TRANSIENTE  
2.- LOS PARABRAYOS SE CONECTARAN EN TERMINALES  
Y1 E Y2 DE CADA FASE

|                   |  |  |                |         |                                                                                 |                   |        |          |          |                |  |  |
|-------------------|--|--|----------------|---------|---------------------------------------------------------------------------------|-------------------|--------|----------|----------|----------------|--|--|
|                   |  |  | 8              | JUN.12  | REEMPL. MED. MICOM301 POR ION 7850/7330                                         | JCLT              | RHG    | MLF      | CMO      |                |  |  |
|                   |  |  | 7              | NOV.08  | PROTECCION UR                                                                   | JCLT              | RHG    | MLF      | CMO      |                |  |  |
|                   |  |  | 6              | OCT.07  | SE REEMPLAZAN UR Y RI POR SISTEMA TERMINAL DE CONTROL                           | JCLT              | EDA    | MLF      | CMO      |                |  |  |
|                   |  |  | 5              | FEB.02  | AS BUILT Y SE CAMBIO NOMBRE DE S/E                                              | S.A.N.            | R.S.L. | S.CH.OH. | P.V.V.   |                |  |  |
|                   |  |  | 4              | MAY.01  | ACTUALIZADO                                                                     | S.A.N.            | R.S.L. | S.CH.OH. | P.V.V.   |                |  |  |
|                   |  |  | 3              | ENE.01  | EN NEUTRO AUTOTR. SE INDICO RELE 51-51N(F512) MICOM P122 Y ACTUALIZO A LA FECHA | S.A.N.            | R.S.L. | S.CH.OH. | P.V.V.   |                |  |  |
|                   |  |  | 2              | OCT.00  | REVISION SEGUN DIAGRAMAS DE CONTROL Y PROTECCIONES                              | RRF               | RSL    | LCV      | PVV      |                |  |  |
|                   |  |  | 1              | JUL. 12 | REEMP. 21-21N-S1 EPAC 3522 POR UR-D90+                                          | JCLT              | RHG    | MLF      | CMO      |                |  |  |
| TRA01-30-51-02-00 |  |  | Nº             | FECHA   | DESCRIPCION                                                                     | DIBUJO            | DISEÑO | REVISO   | APROBADO |                |  |  |
| PLANOS AFINES     |  |  | MODIFICACIONES |         |                                                                                 | TRA01-30-51-01-00 |        |          | 9        | FECHA JUN.2020 |  |  |

PROYECTO: ALIMENTACION A ANTOFAGASTA

OBJETO: S/E ESMERALDA

DETALLE: DIAGRAMA UNILINEAL GENERAL 220 - 110 kV

PLANO Nº

MOD. 9

FECHA