


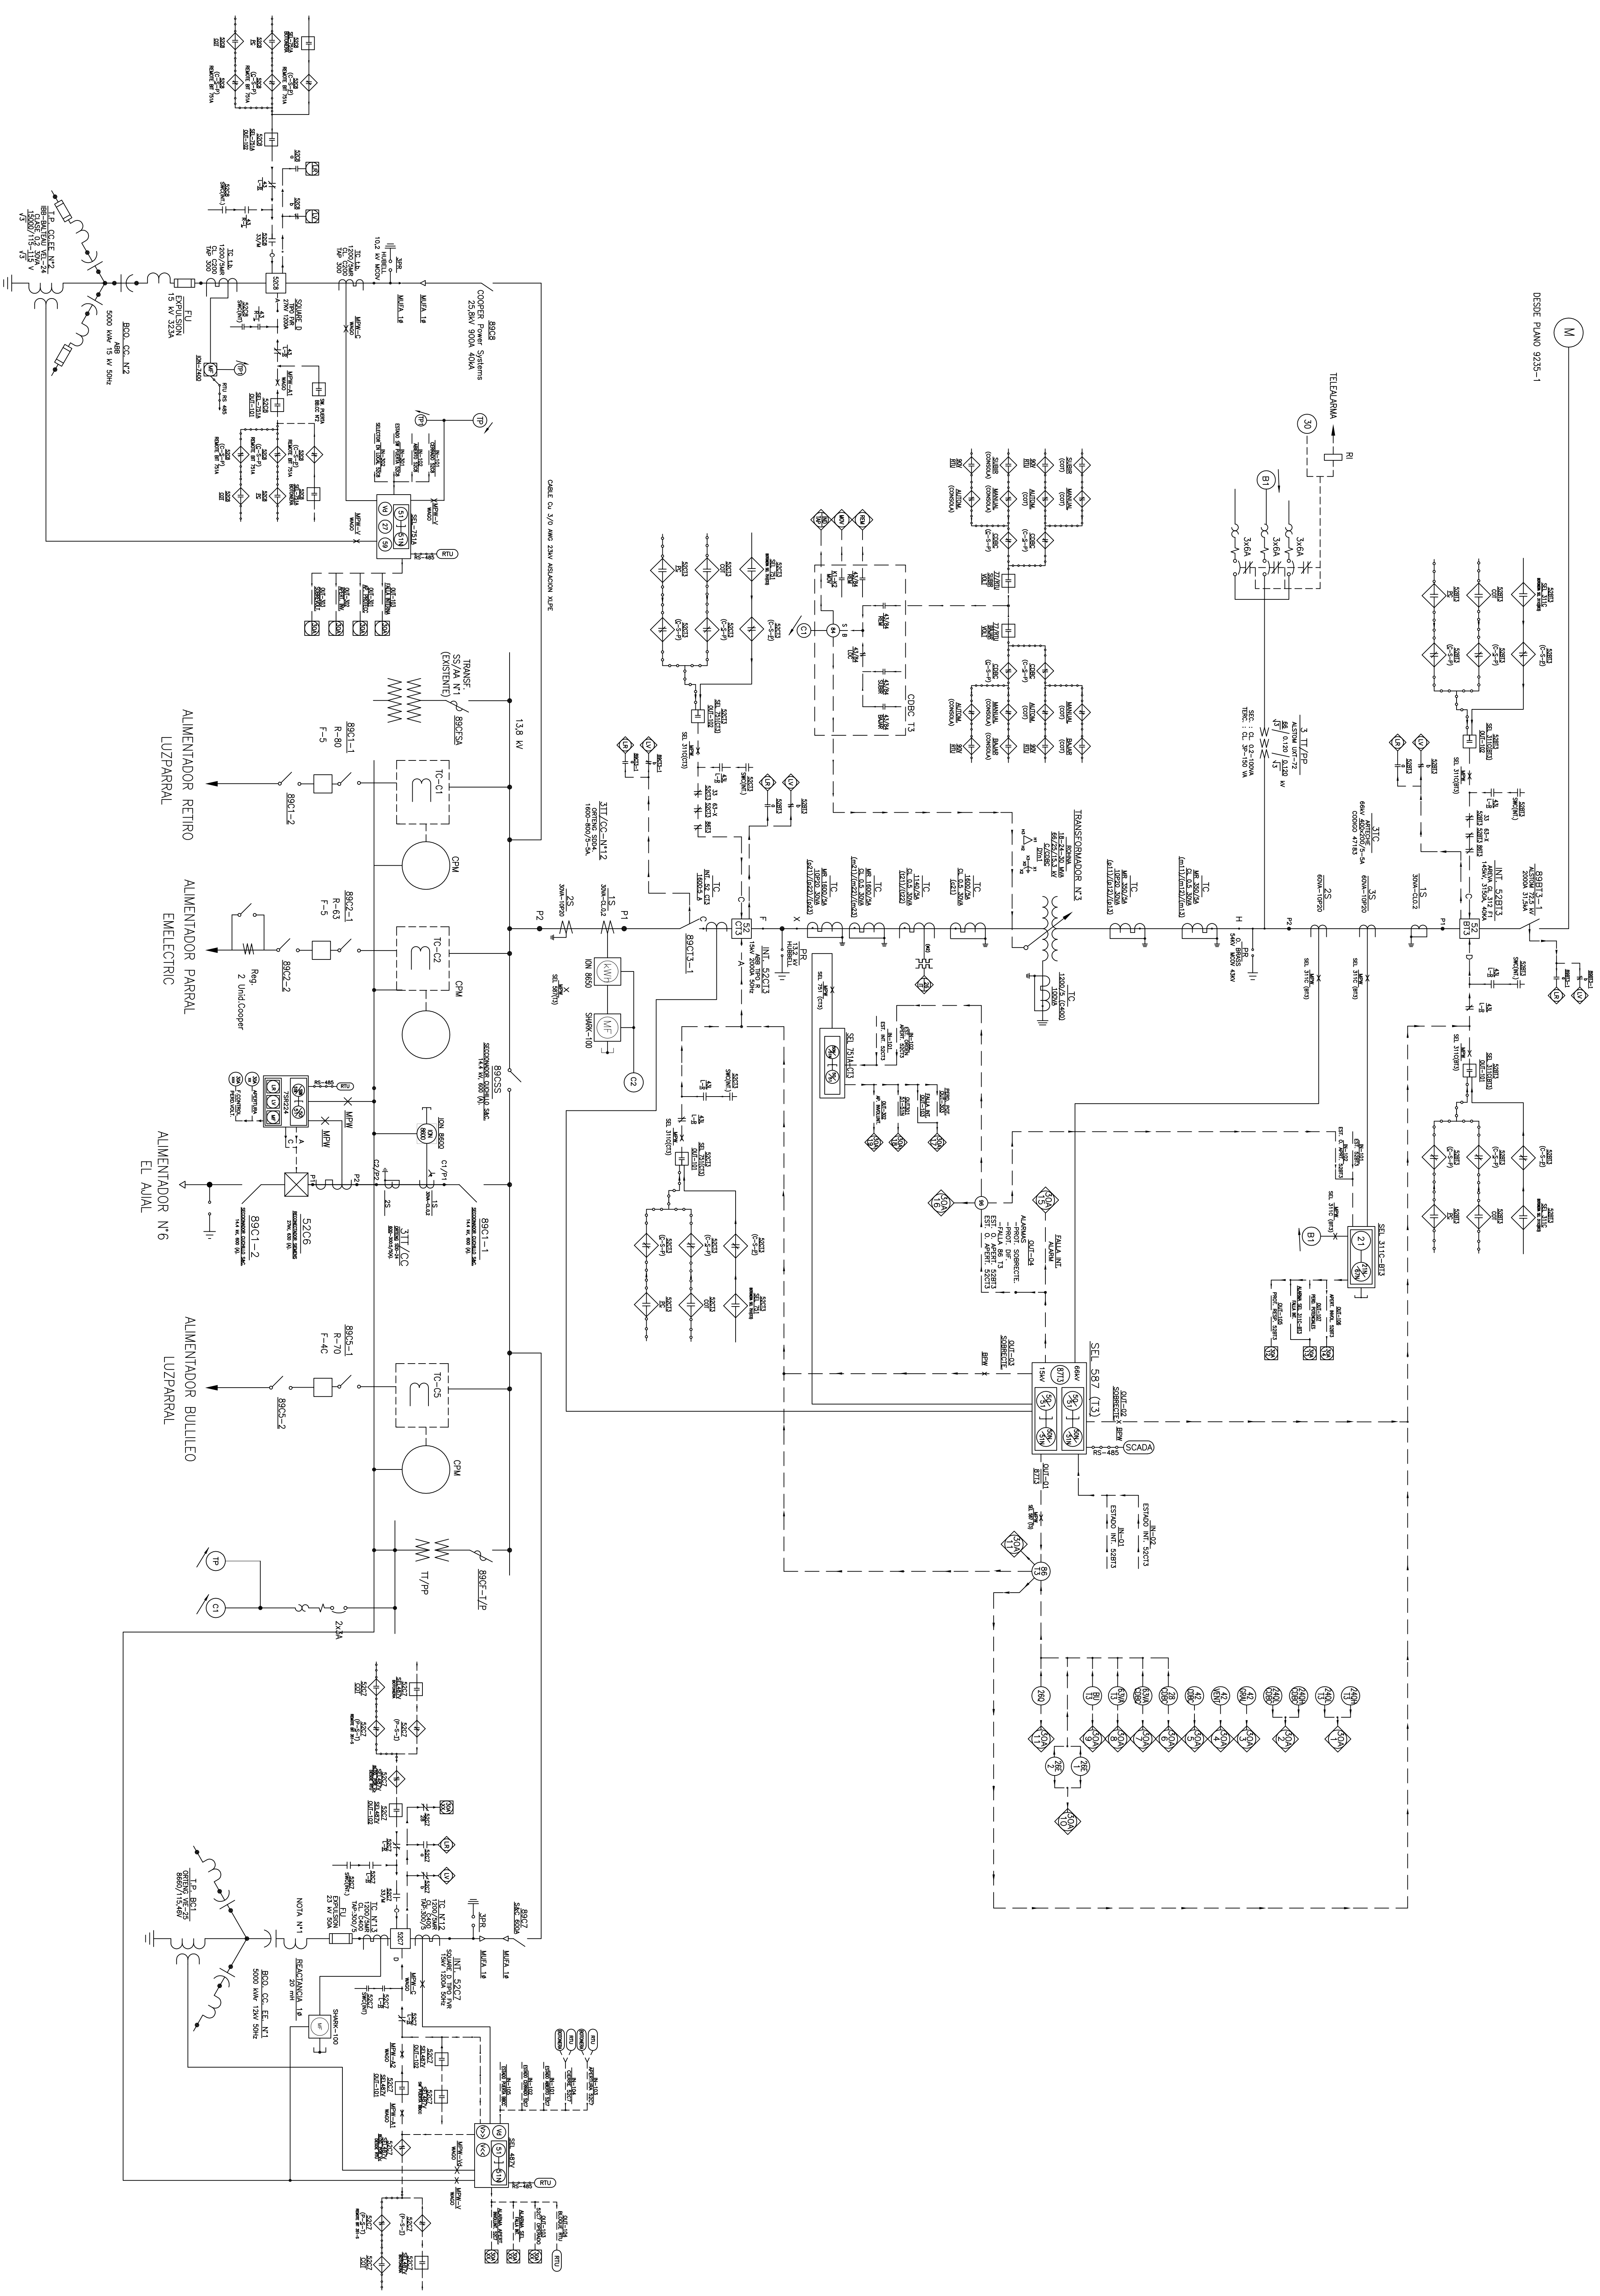

SUBSTACION PARALELA 154/66/13.2 KV				CGE				DIAGRAMA UNILINEAL FUNCIONAL			
9	INSTALACION DEB. N° 154KV TAV	154.3	J.F.G.	09-2017				PROYECTO	PAE	REVISADO	FECHA
8	PROYECTO MONTEO DE POTENCIA RELEVADO DE TRANSFORMADOR N° 3	154.3	J.F.G.	09-2017				PROYECTO	PAE	REVISADO	FECHA
6	IMPLEMENTACION MONTEO ALIMENTADOR N° 6 EL ALUM.	154.3	J.F.G.	09-2017				PROYECTO	PAE	REVISADO	FECHA
P R O Y E C T O S				PROY	APROBADO	FECHA	AS	REB	ZONA		
									MAYLE		

- NOTAS
- 1.- SE RECONSTRUYEN TRANS. DE CORRIENTE Y SE RECONSTRUYEN TRANS. DE POTENCIA EN EL MONTEO DE POTENCIA RELEVADO DE TRANSFORMADOR N° 3.
 - 2.- EL SISTEMA DE MONITOREO Y TELECOMANDO A DISTANCIA A TRAVES DEL CENTRO DE DESPACHO DE C.A.E. CUANDO SE PROYECTA EN EL MONTEO DE POTENCIA RELEVADO DE TRANSFORMADOR N° 3.
 - 3.- FALTA INFORMACION TECNICA CERTIFICADA DE FABRICA DEL EQUIPO, REPOSICIONADO DE EQUIPO.
 - 4.- NO SE DISPONE DE INFORMACION TECNICA DE LOS EQUIPOS DE 13.8 KV.