




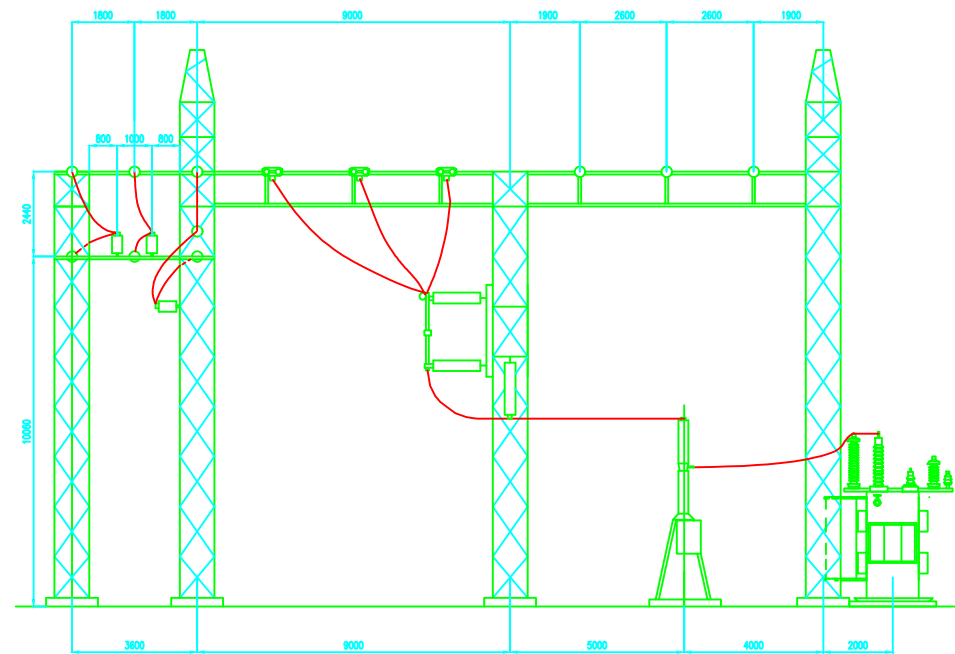


CORTE A
ESCALA: 1:100

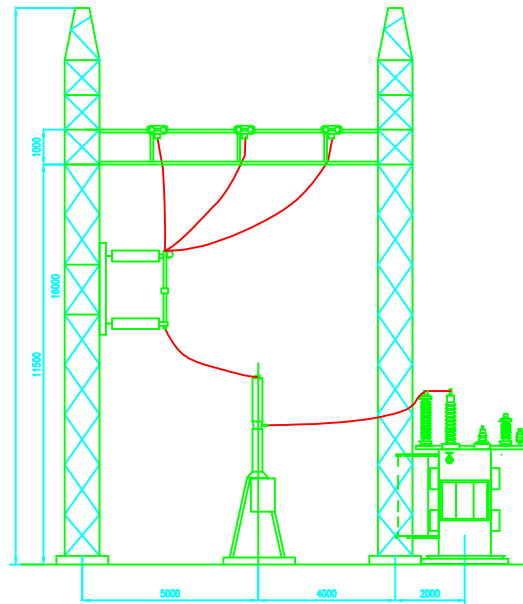


CORTE C
ESCALA: 1:100

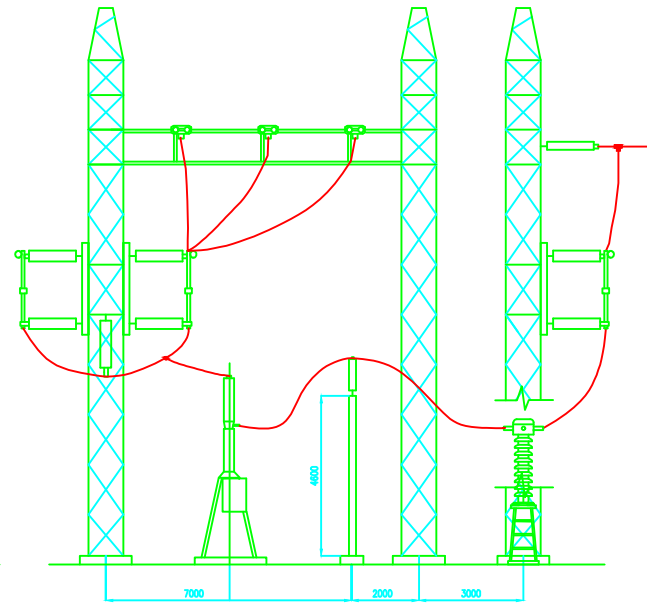


CORTE F
ESCALA: 1:100

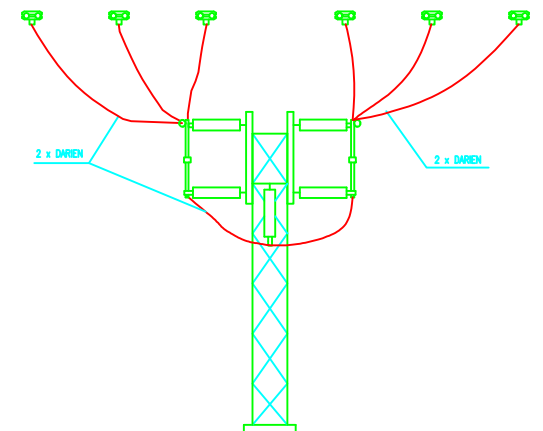


CORTE O
ESCALA: 1:100

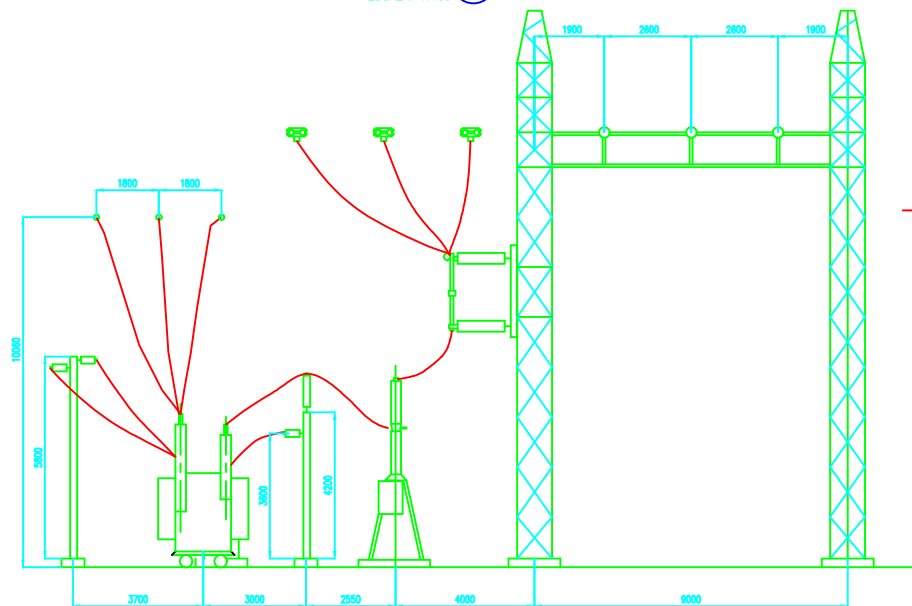


CORTE B
ESCALA: 1:100

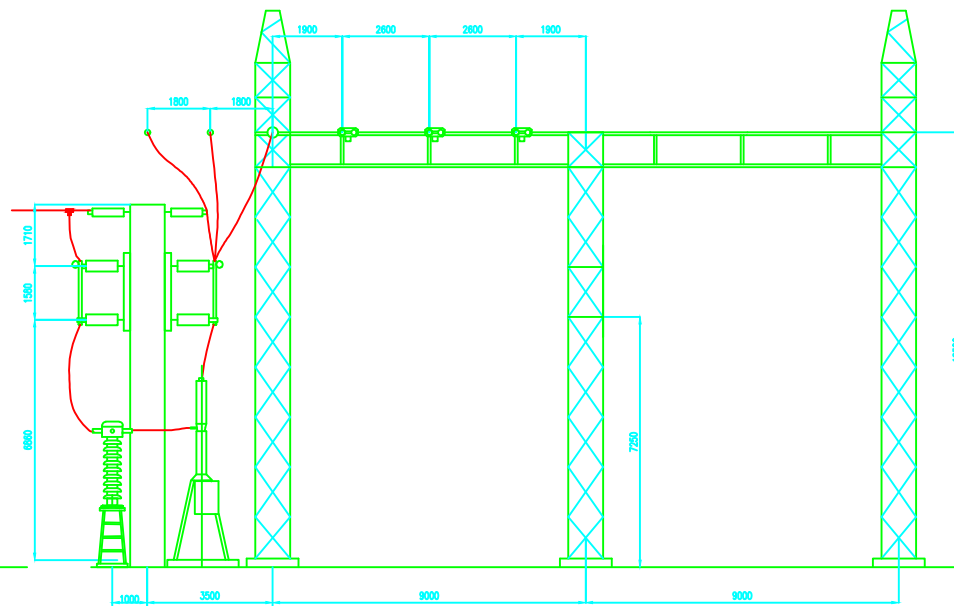


CORTE E
ESCALA: 1:100

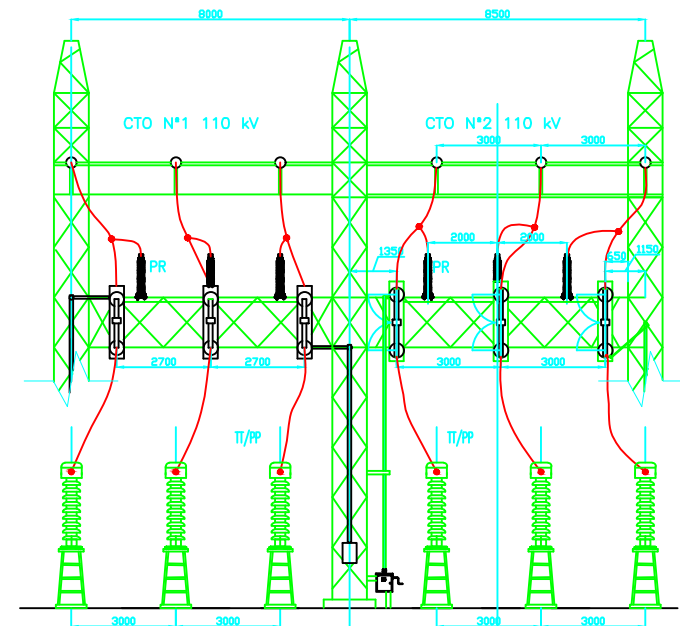


CORTE H
ESCALA: 1:100

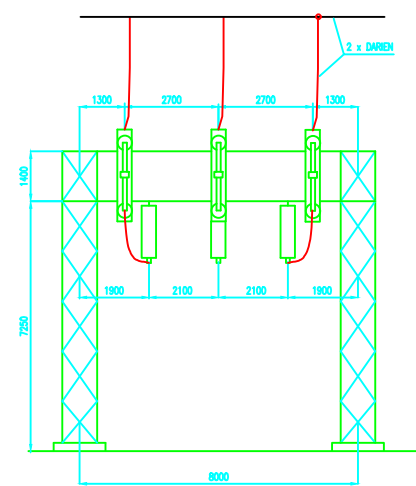


CORTE J
ESCALA: 1:100

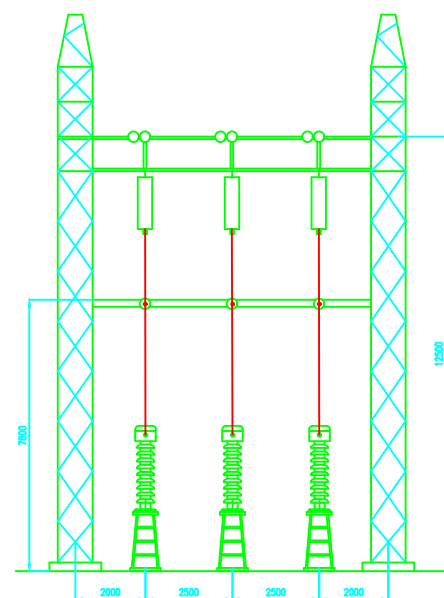


CORTE G
ESCALA: 1:100

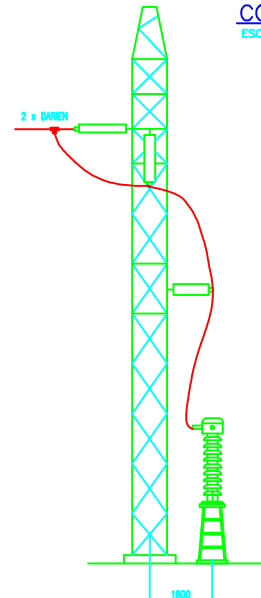

CORTE K
ESCALA: 1:100

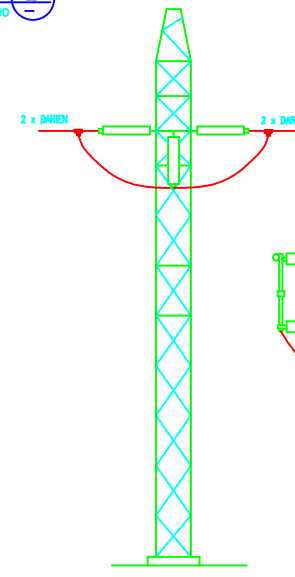

CORTE L
ESCALA: 1:100

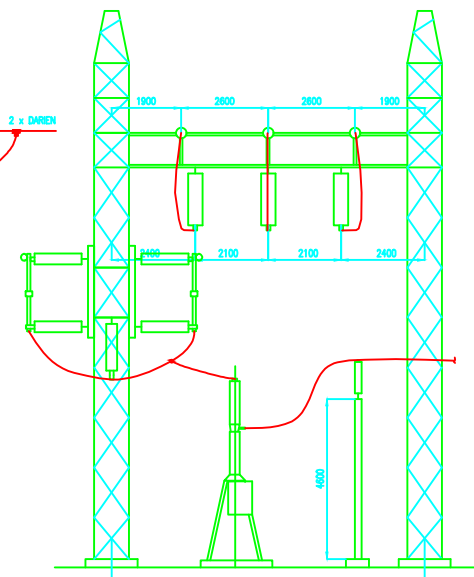

CORTE M
ESCALA: 1:100

REFERENCIAS:

SE18-PL-ED-001-00-R06 DISPOSICION EQUIPO ELECTICO - PLANTA
SE18-PL-EU-001-00-R11 DIAGRAMA UNILINEAL

NOTAS:

TODAS LAS MEDIDAS SON EN MILIMETROS SIC.

00 AGO-17 NORMALIZACION DE PLANOS				INGESAT INGESAT CHILQUINTA	
Nº	FECHA	MODIFICACIONES	POR	REV	APROBADO
			S/E 110/66/23/12 kV SAN ANTONIO DISPOSICION EQUIPO ELECTICO SECCIONES		
DIB: O. C. H. PROY: S. J. L. REV: C. M. F.			Nº PLANO : SE18-PL-ED-005-01-R00		
SUBGERENCIA INGENIERIA			FECHA: ESCALA: 1 : 100		LAM: 01 DE 02