

PLANO Nº
C 201-52e-1L1


VISTA A-A
ESC. 1:75

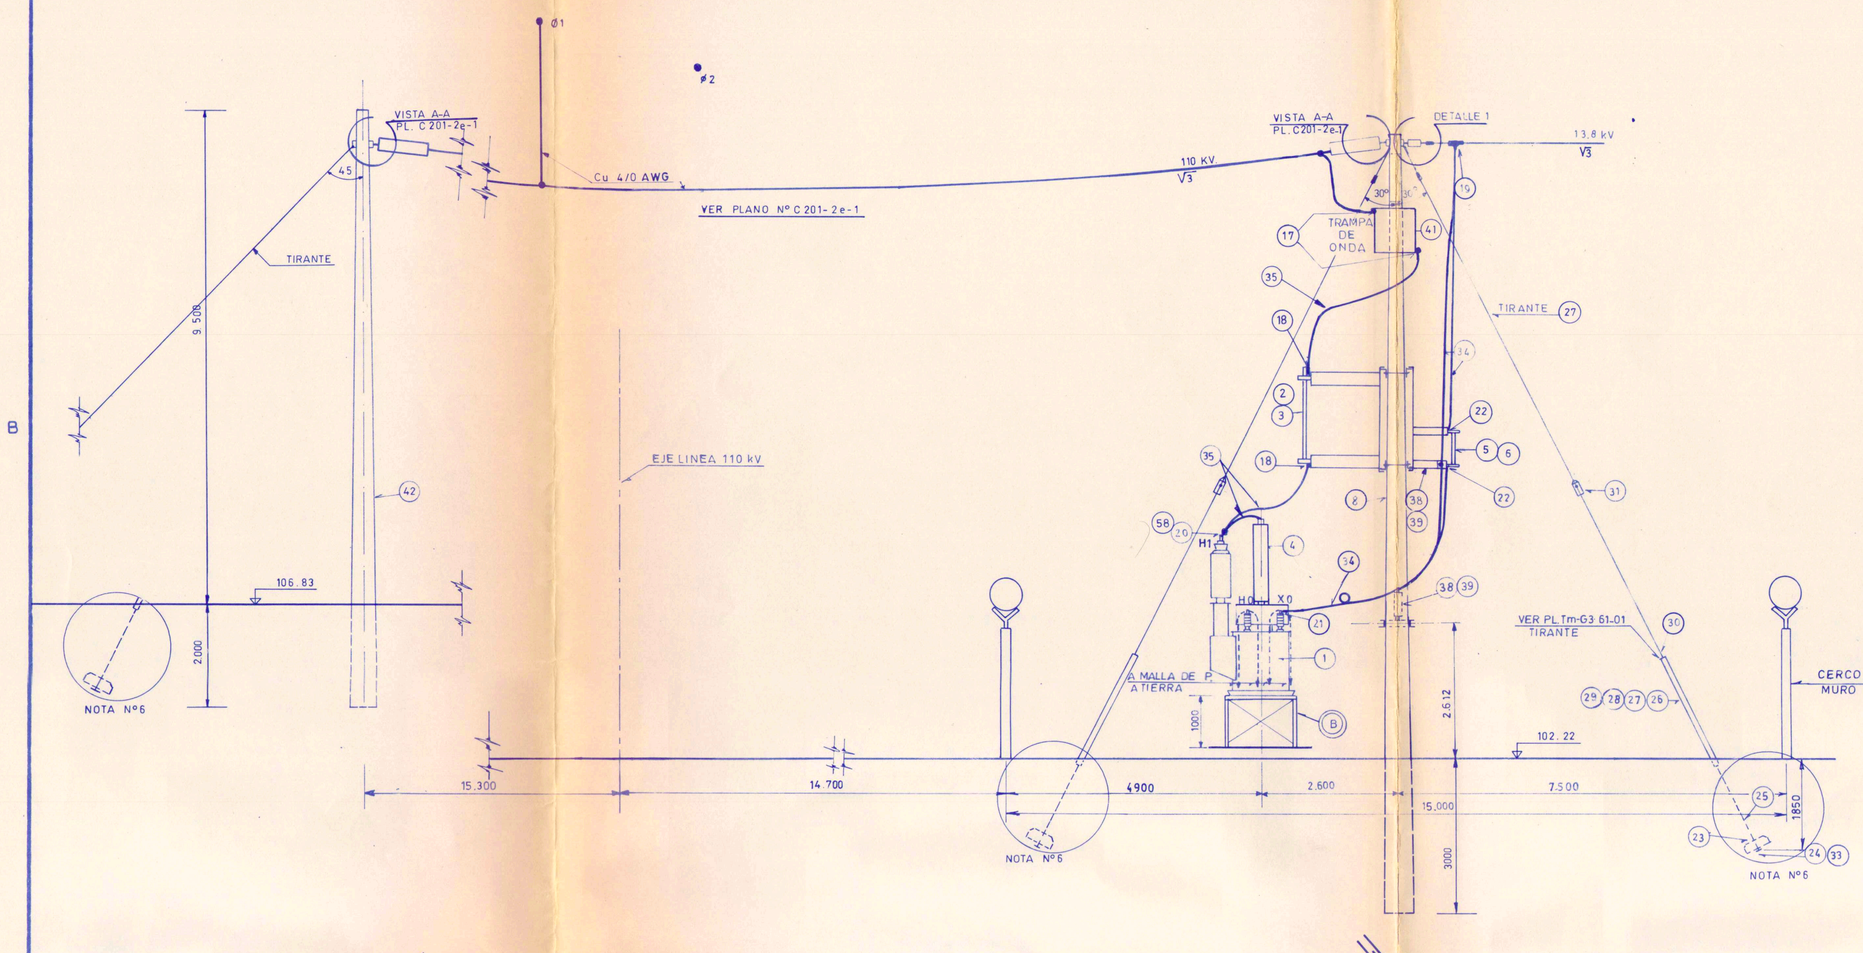


VISTA B-B
ESC. 1:75

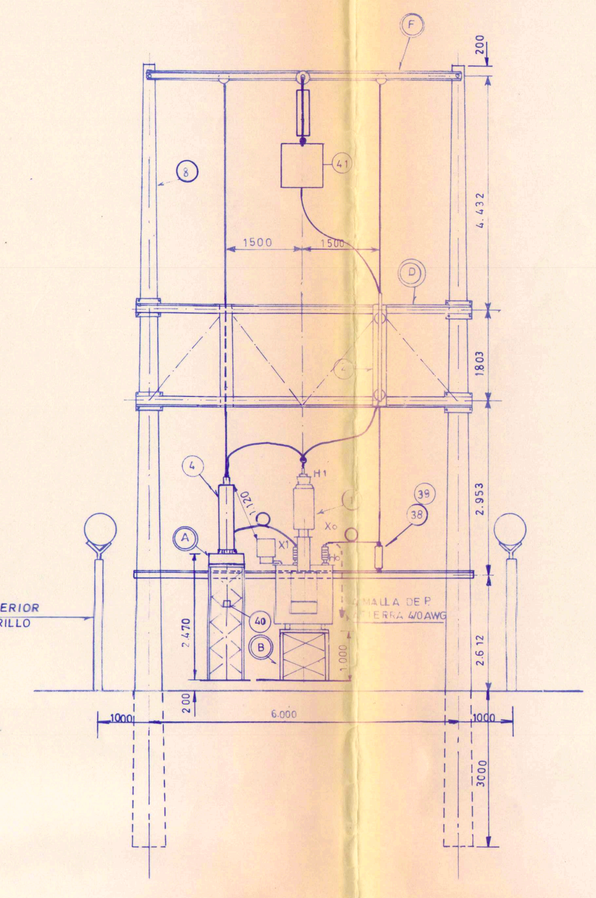


VISTA C-C
ESC. 1:75

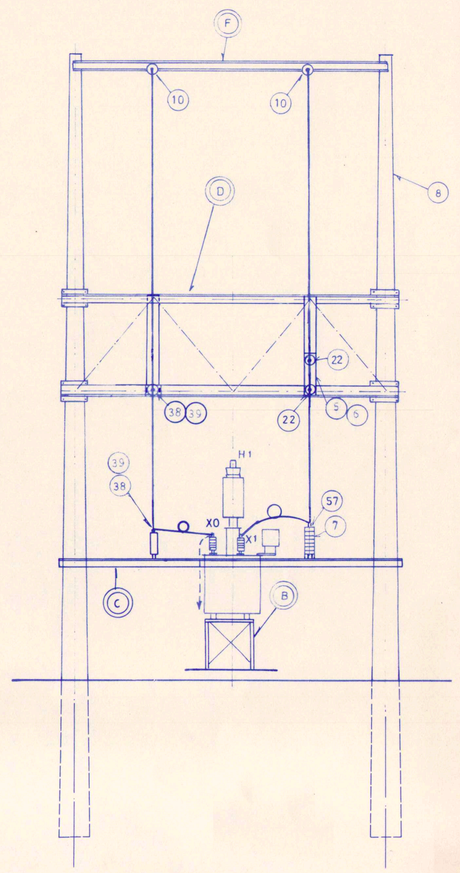


DETALLE DE UBICACION
ESCALA 1:500

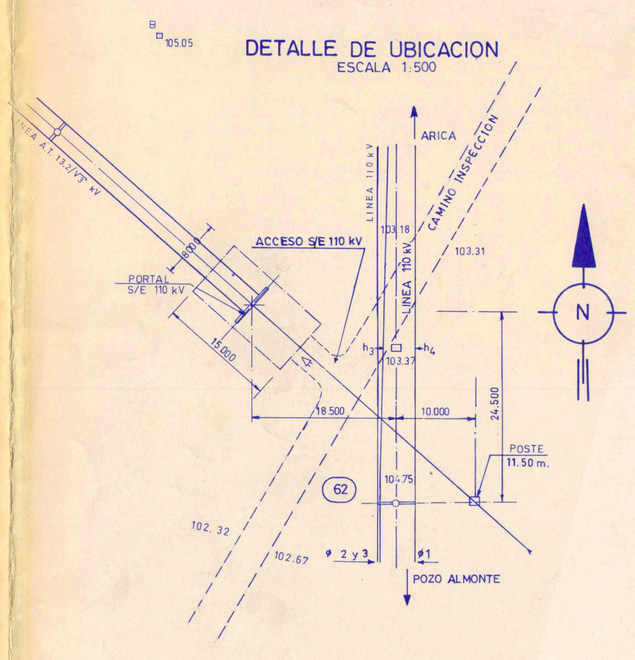

PLANTA
ESC. 1:75

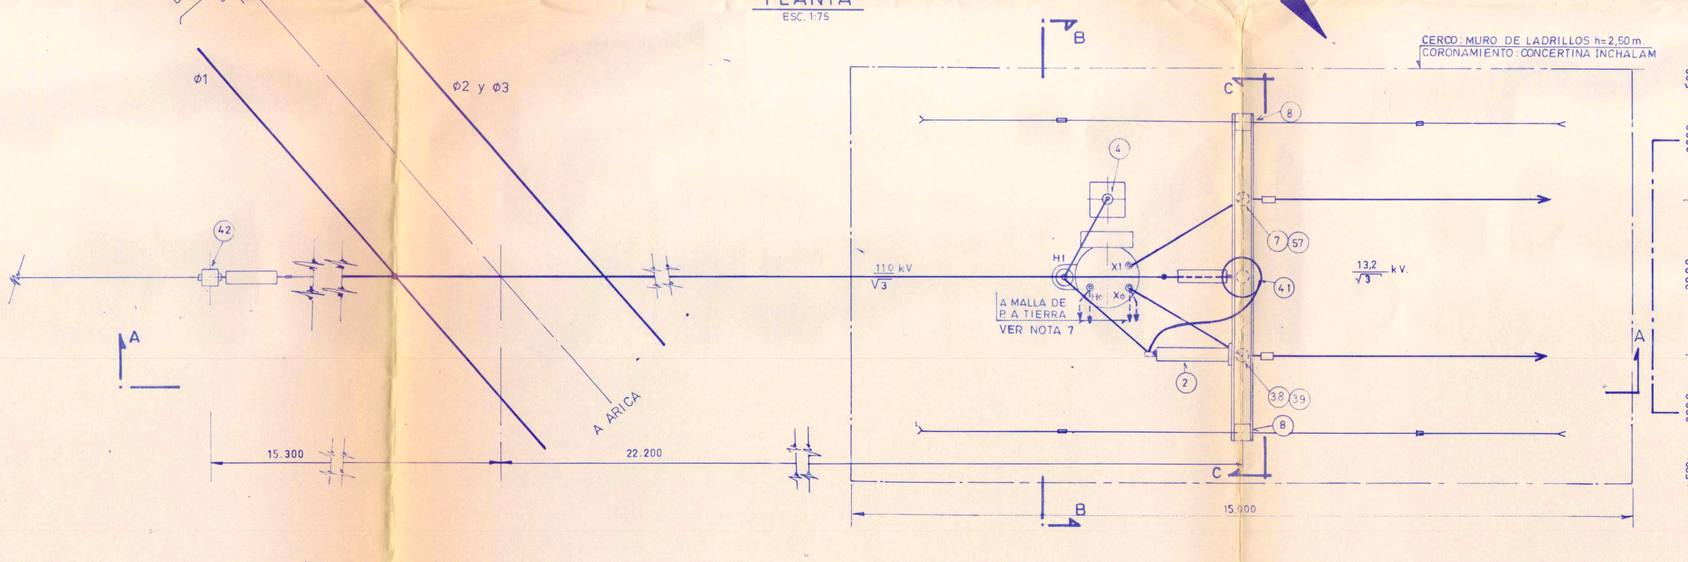

PLANTA
CERCO Y MALLA DE PUESTA A TIERRA
ESC. 1:75

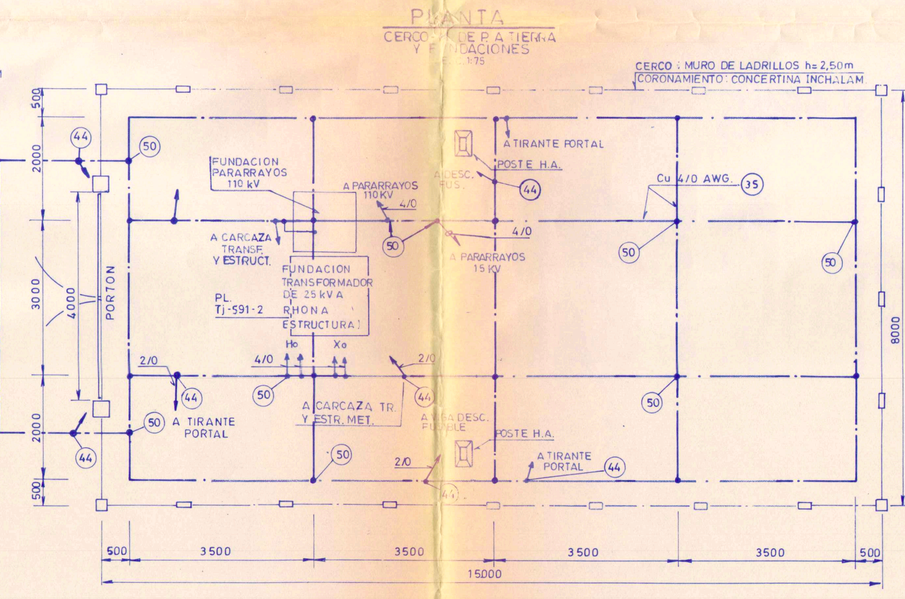

NOTAS

1- ~~DEBERA REVISARSE EL DISEÑO DE ESTA MA-~~
~~CUANDO SE DISPONGA DE LOS VALORES DE RE-~~
~~TIVIDAD CORRESPONDIENTES.~~

2- LA MALLA DE P.A.T. DEBERA ENTERRARSE A UNA PROFUNDIDAD DE 60cm DESDE EL NIVEL NATURAL DEFINITIVO.

3- TODOS LOS EQUIPOS ELECTRICOS, ESTRUCTURAS METALICAS ETC. DEBERAN CONECTARSE A LA MALLA DE P.A.T. AUNQUE NO SE INDIQUE EXPRESAMENTE EN ESTE PLANO, EN FORMA INDIVIDUAL

4- TODAS LAS UNIONES ENTRE CONDUCTORES DE LA MALLA Y DE ESTA A LOS EQUIPOS Y ESTRUCTURAS DEBERA EJECUTARSE CON UNIONES DE TERMOFUSION, EXCEPTO EN AQUELLOS CASOS QUE EL DISEÑO DEL EQUIPO INDIQUE PRENSAS DE CONEXION.

5- A PARTIR DEL TERRENO COMPACTADO, LA SUPERFICIE DEL PATIO DE 110kV DEBERA CUBRIRSE CON UNA CAPA DE 15cm DE ESPESOR, DE GRAVA, CHANCADO O CONCHUELA LAVADA DE 3/4" A 1"

6- LOS MUERTOS DE ANCLAJE Y TIRANTES SE INSTALARAN SEGUN PLANO Tj-323-1L1.


7- LOS BUSHINGS Ho y Xo DEL TRANSFORMADOR, DEBERAN CONECTARSE A LA MALLA DE PUESTA A TIERRA MEDIANTE DOS CHICOTES DE CONEXION INDEPENDIENTES PARA CADA BUSHING.

8- COLOCAR LETREROS ESPECIALES DE ADVERTENCIA, CONTRA DESCONEXION DE PUESTA A TIERRA DE LOS TRANSFORMADORES, ESTANDO ESTOS ENERGIZADOS

9- LA CONEXION DE LOS BUSHINGS DE NEUTRO DE LOS TRANSFORMADORES A LA MALLA DE PUESTA A TIERRA, DEBERA EFECTUARSE CON PRENSAS O CONECTORES QUE ASEGUREN UNA BUENA CONEXION LIBRE DE CORROSION, LA CUAL DEBERA TENER UN MANTENIMIENTO PERIODICO.

10- PREVIO A LA ENERGIZACION, DEBERA MEDIRSE EL VALOR DE LA RESISTENCIA DE LA MALLA DE PUESTA A TIERRA, EN CADA UNA DE LAS SUBESTACIONES.


DETALLE 1
S/ESC.

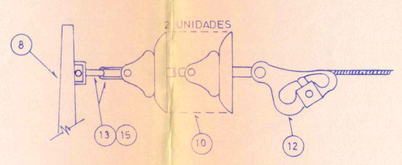

DISTANCIAS MINIMAS

VOLTAJE	ENTRE FASES	FASE-TIERRA
110 kV	1.800mm	1.250 mm
13,2 kV	350mm	230 mm

DIAGRAMA UNILINEAL SIMPLIFICADO

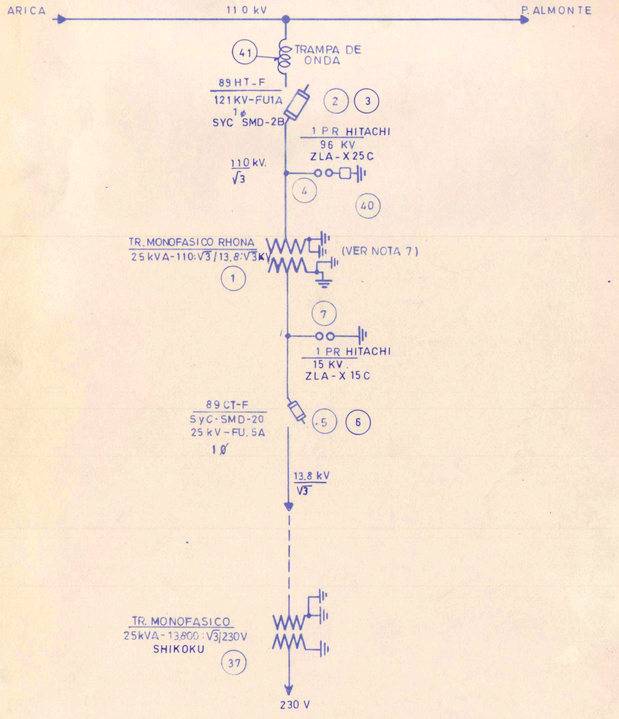

NOTA GENERAL

ESTE PLANO ES VALIDO SOLAMENTE PARA LA S/E MAL PASO.

PLANOS AFINES

PLANO UBICACION Y LEVANT. TAGUIMETRICO. . . . C201-1e-1
LISTA DE PLANOS DEL PROY. ELECTRICO. . . . C201-1e-2L1 y 2L2
- DISP. EQUIPOS, CERCO Y MALLA DE P.A TIERRA Y FUNDACIONES. . . . C201-52e-1L2 Y L3
- IDEM. . . . LISTA DE ESTRUCTURAS. . . . C201-52e-1L4
-PORTON METALICO PARA S/E. . . . Tg-89-26
-PORTAL 110/13.8 kV VIGAS FAB. Y MONTAJE. . . . C201-70j-1 Y 2
-TRANSF. DE 25 kVA ESTRUCTURA. . . . Tj-591-1
- IDEM FUNDACION. . . . Tj-591-2
-CIERRO EXTERIOR PLANTA ELEVACION ETC. . . . C201-80g-1
-ENMALLE 110 kV, PERFIL, TENSADO, DET. . . . C201-2e-1
-PORTAL REMATE, PL. DISEÑO. . . . Tj-323-1L1

SIMBOLOGIA

- ◯ ITEM LISTA DE MATERIALES
- ◯ ID. . ESTRUCTURAS
- Nº ESTRUCTURA LINEA 110 kV.

Nº	FECHA	MODIFICACIONES	EJECUTO	REVISO	APROBO
4	SEPT.'87	SE ACTUALIZO CONFORME INSPECCION TERRENO.	R.S.L.		
3	MAR.'87	SE CAMBIO CONDUCTOR DE ENMALLE ALLIANCE POR 4/0 AWG.	R.S.L.		
2	DIC.'86	ACTUALIZO, UBIC., PLANTA, VISTAS, NOTAS, PLS AFINES Y AGR. IT. 41 Y 42	R.S.L.		
1	DIC.'85	SE MODIFICO DISP. DE EQUIPOS Y SE AGREGO VIGA EN PORTAL Y NOTA GRAL.	J.R.S.		

ESC. 1:75
TIPO B

PROYECTO: SISTEMA INTERCONECTADO NORTE GRANDE
OBRA: S/E MAL PASO
DETALLE: DISPOSICION DE EQUIPOS MALLA DE PUESTA A TIERRA Y FUNDACIONES

ENDESA
EMPRESA NACIONAL DE ELECTRICIDAD S.A. CHILE

FECHA	PLANO Nº	HOJA
AGR. 84	C201-52e-1L1	4

DIBUJO	PROYECTO	CONTROLO	APROBO	MICROFILM	Nº ARCHIVO
C.S.P.	J.R.S./1EOF				B5-23.203