
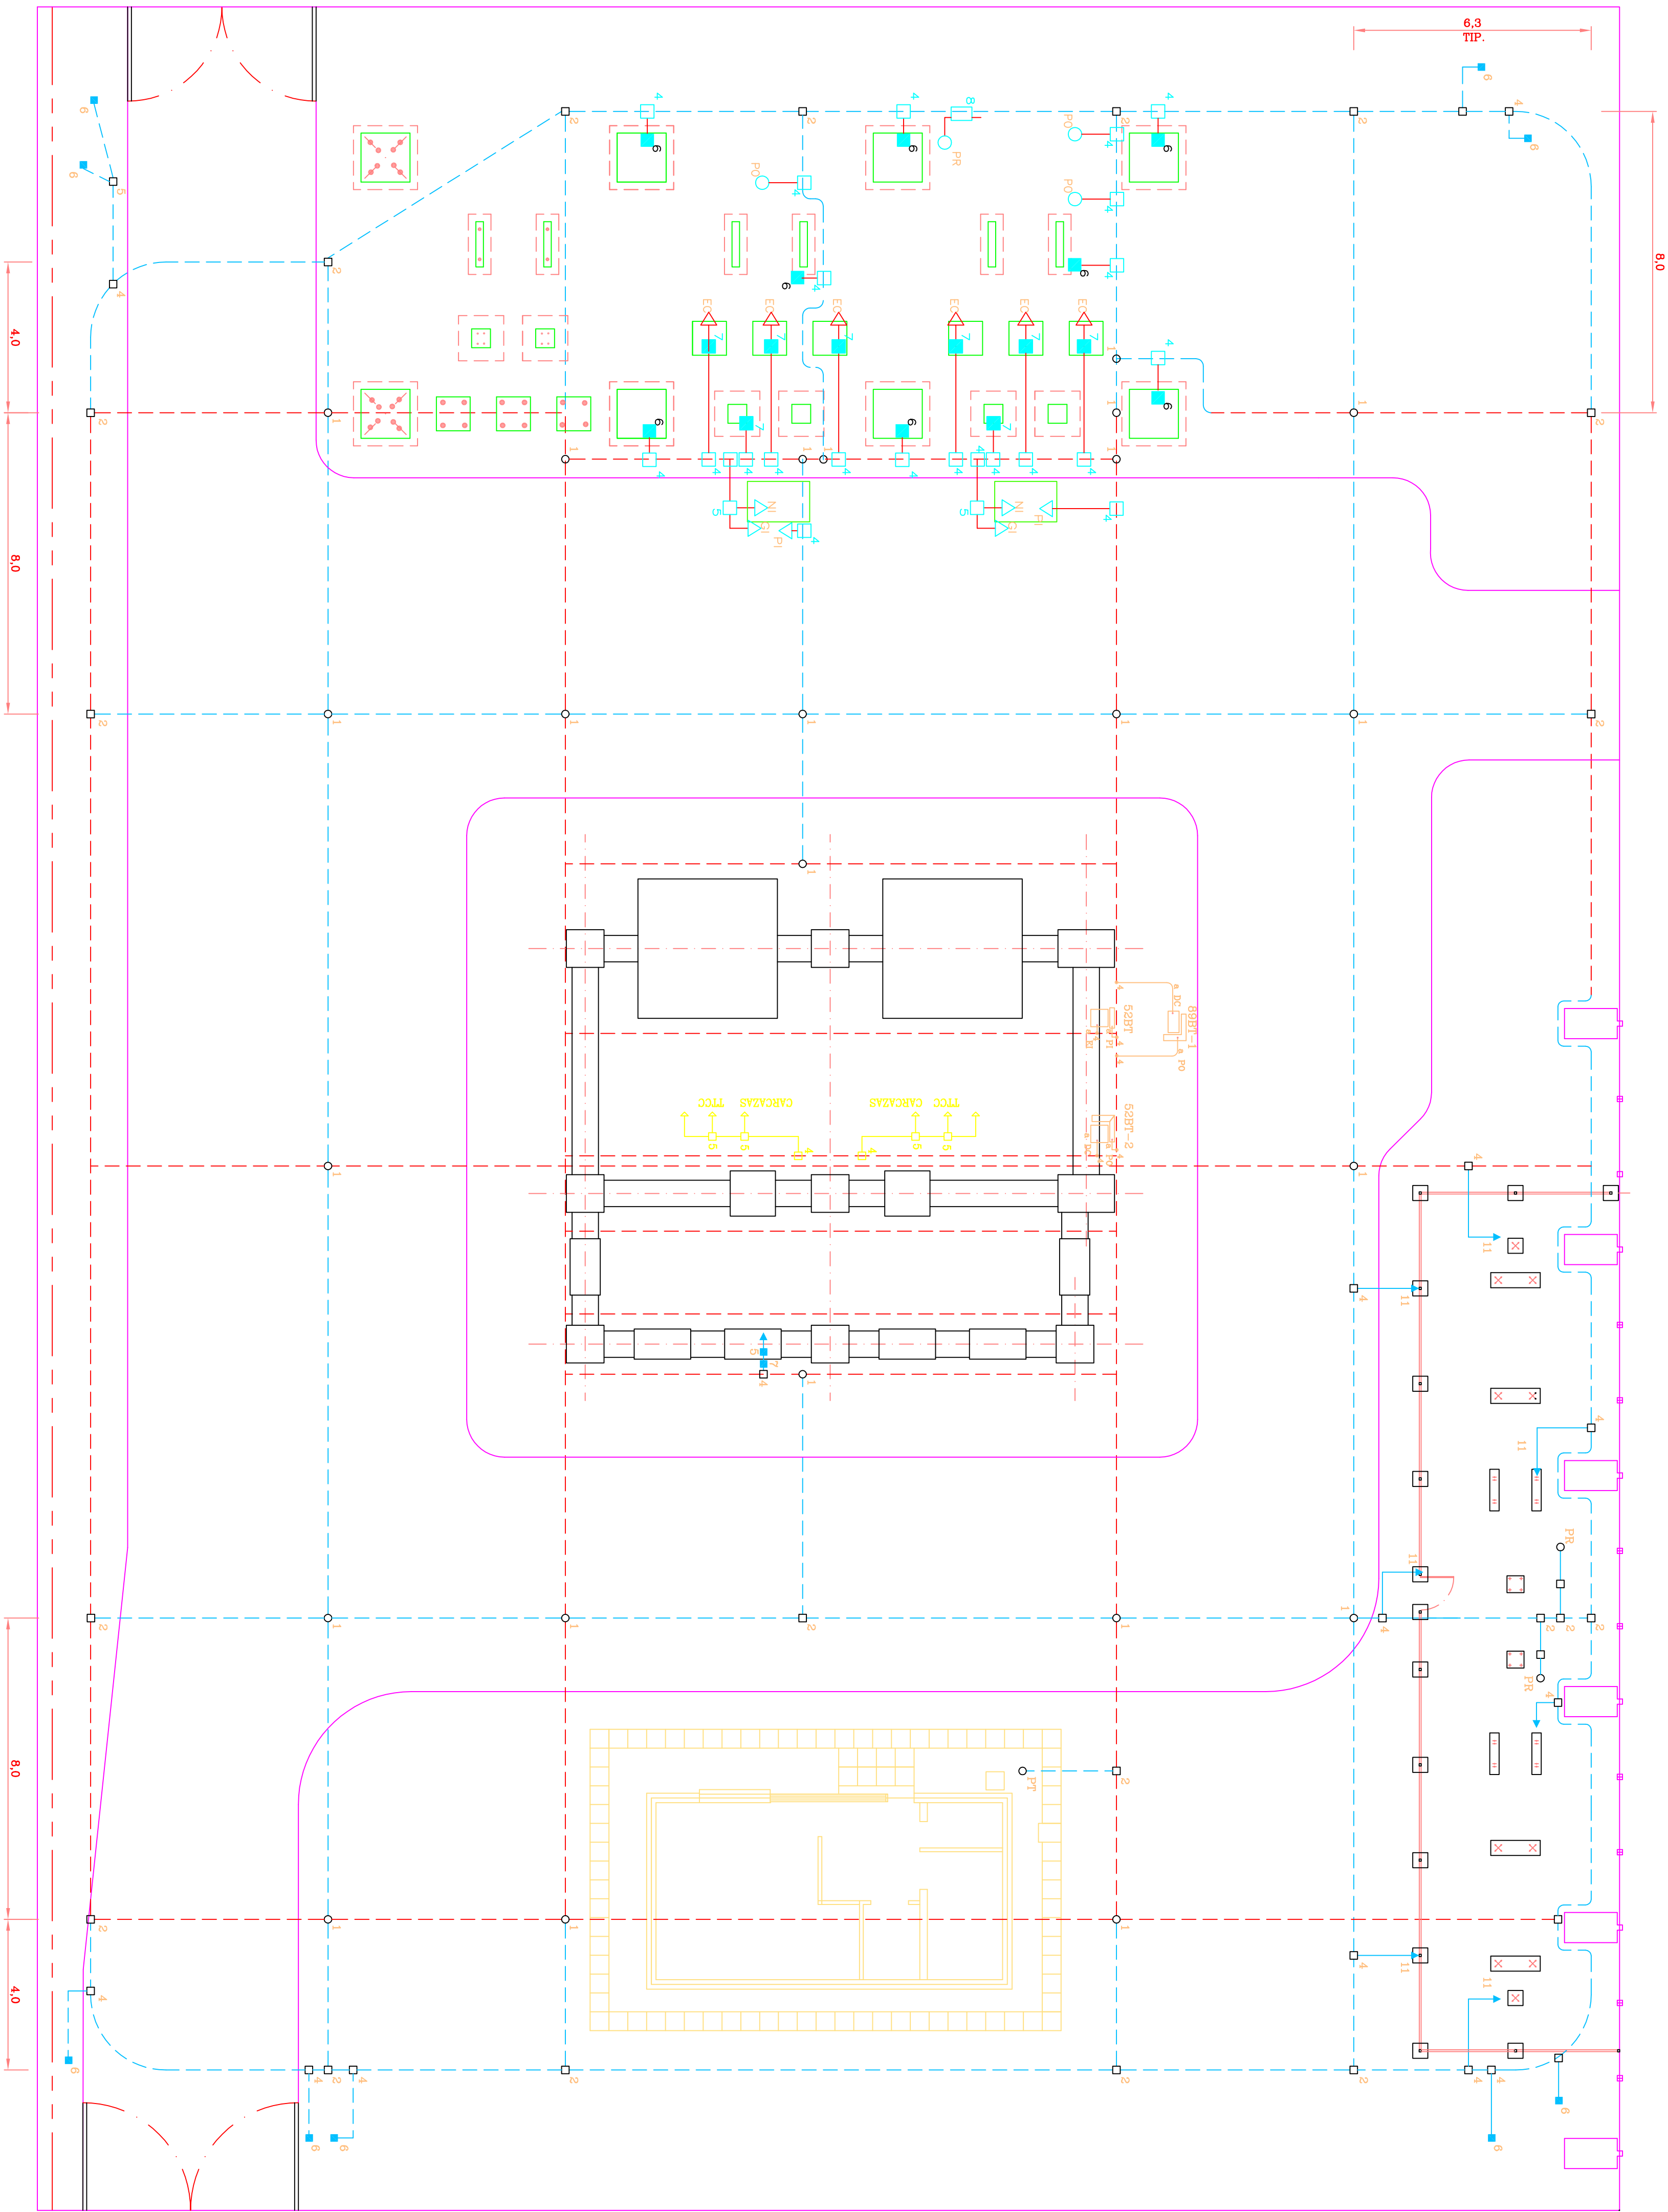


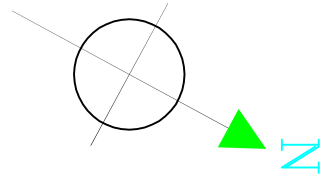

8.0
4.0

NOTAS

- 1.- TODAS LAS DIMENSIONES SON EN METROS, EXCEPTO DONDE SE INDICA
- 2.- LOS NUMEROS QUE APARECEN EN LOS CIRCUITOS COORES-PONDEN A LOS NUMEROS DE LOS DETALLES DEL PLANO N° 7015-X

SIMBOLOGIA

--- = MALLA DE TIERRA EXISTENTE

REFERENCIAS

- 4204-P MALLA DE TIERRA EXISTENTE - DISPOSICION GENERAL
- 7015-X MALLA DE TIERRA - DETALLES TIPICOS
- 7715-P POSTE PARA SISTEMA DE VIGILANCIA - DETALLES DE FABRICACION Y MONTAJE
- 7732-P POSTE CHAPA DE CONEXIONES-DETALLES DE FABRICACION Y MONTAJE
- 8086-X INSTALACION DE DOS BANCOS DE CONDENSADORES TI-PO A - FUNDACIONES Y CIERRO

PLANTA

DISPOSICION GENERAL

ESCALA 1 : 100

SE CHIGUAYANTE 66/15 kV				PLANO N°	
MALLA DE TIERRA				7972-A1	
DISPOSICION GENERAL					
REVISO	MAA	DIBUJO	MAA		
APROBADO	PROYECTO	PROYECTO	HRA		
MODIFICADO	FECHA	FECHA	ESCALA	1 : 200	
TRANSNET					