


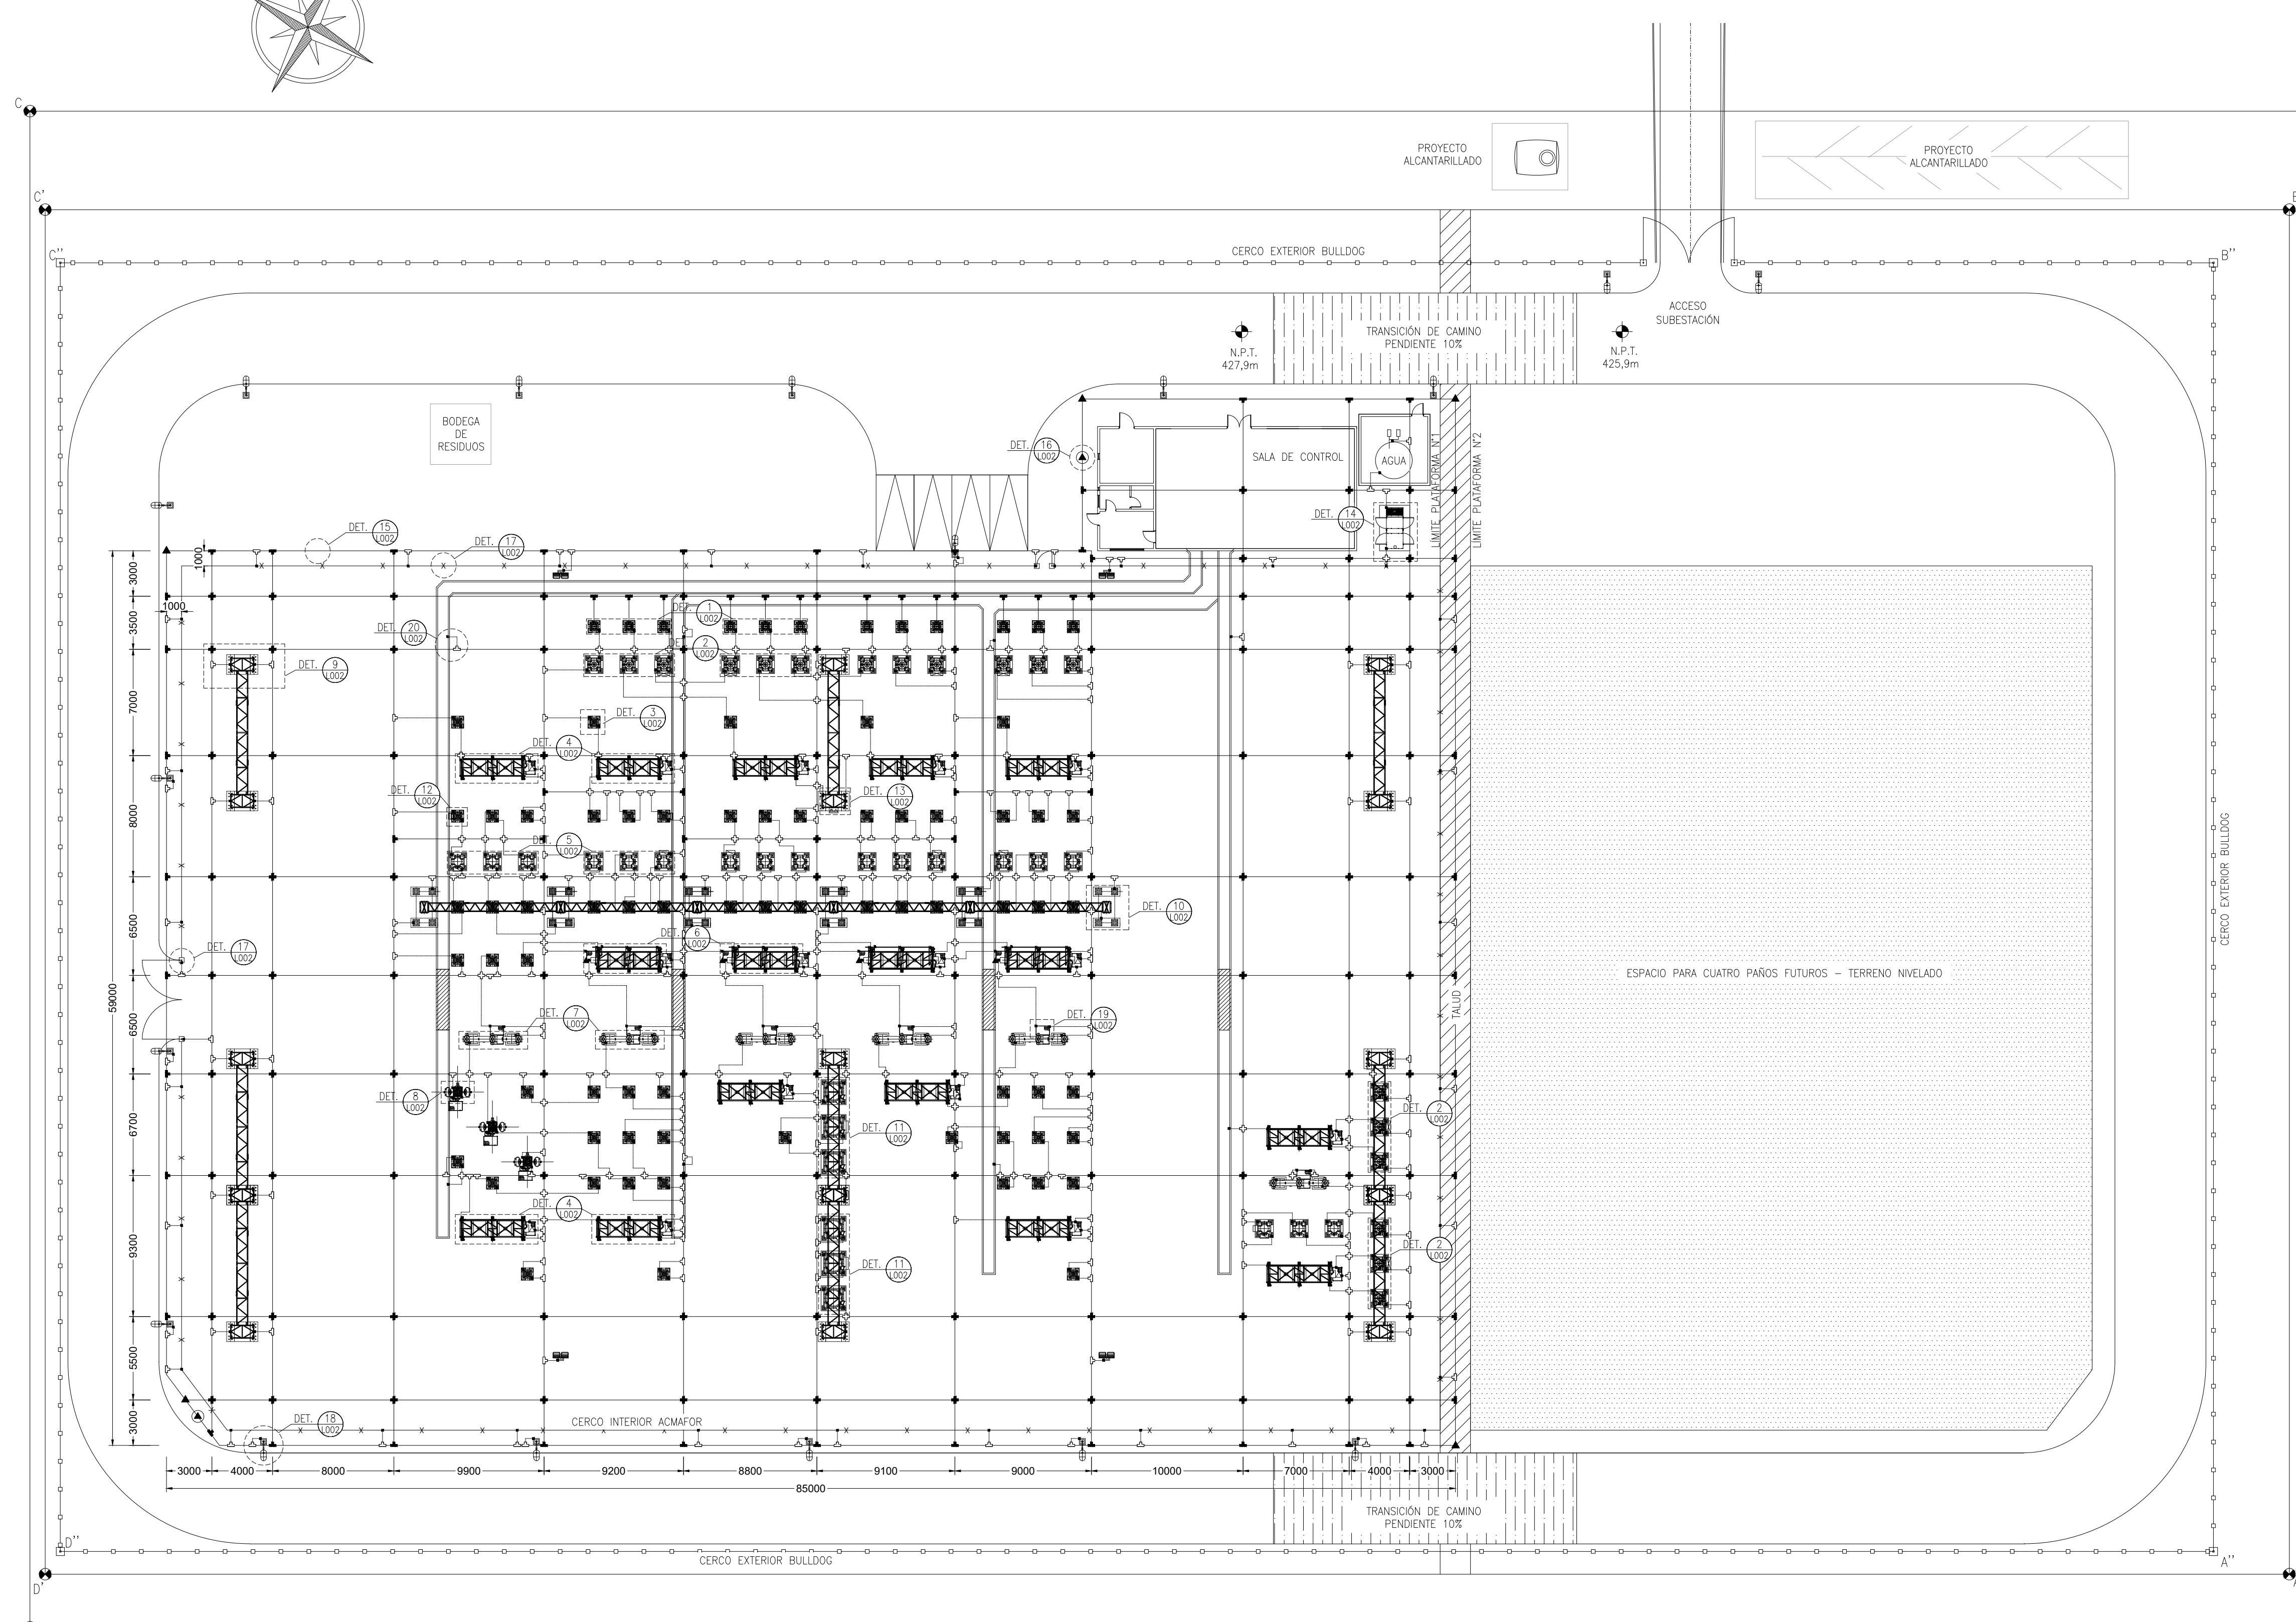

	CABLE DE COBRE DESNUDO #4/0 AWG
	CABLE DE COBRE DESNUDO #2/0 AWG
	UNIÓN TIPO "X" PARA CABLES #4/0 AWG - #4/0 AWG
	UNIÓN TIPO "X" PARA CABLES #4/0 AWG - #2/0 AWG
	UNIÓN TIPO "T" PARA CABLES #4/0 AWG - #4/0 AWG
	UNIÓN TIPO "T" PARA CABLES #4/0 AWG - #2/0 AWG
	CONEXIÓN A EQUIPO O ESTRUCTURA
	BARRA COPERWELD #3/4"x300mm
	CAMARA DE REGISTRO
	CAJA DE AGRUPAMIENTO TTCC
	CAJA DE AGRUPAMIENTO TIPP
	CAJA DE AGRUPAMIENTO DE CALEFACTORES

SE315T003-P-EE-00-001	DIAGRAMA UNILINEAL GENERAL
SE315T003-P-EE-01-001-L001	DISPOSICIÓN GENERAL DE EQUIPOS DE PATIO - PLANTA
SE315T003-P-EE-01-001-L002	DISPOSICIÓN GENERAL DE EQUIPOS DE PATIO - PLANTA
SE315T003-P-EE-03-001-L001	CANALIZACIONES DE FUERZA Y CONTROL - PLANTA
SE315T003-P-EE-03-001-L002	CANALIZACIONES DE FUERZA Y CONTROL - PLANTA
SE315T003-P-EE-02-001-L002	MALLA DE PUESTA A TIERRA - DETALLES
SE315T003-P-EE-03-001-L002	MEDIDA DE CALCULO - PUESTA A TIERRA SUBTERRANEA
SE315T003-P-EE-01-004	LISTA DE MATERIALES - PUESTA A TIERRA SOTERRADA
SE315T003-P-EE-02-003	MALLA DE PUESTA A TIERRA SALA ELÉCTRICA - PLANTA Y DETALLES

1. TODAS LAS MEDIDAS ESTÁN EN MILÍMETROS, A MENOS QUE SE INDIQUE LO CONTRARIO. LAS DIMENSIONES PREVALEN SOBRE LA ESCALA DEL DIBUJO.
2. LOS CHICOTES DE CONEXIÓN DESDE LA MALLA BASE HASTA LOS EQUIPOS Y ESTRUCTURAS, SE DEBERÁN REALIZAR CON CABLE #2/0 AWG. EXCEPTO LOS CHICOTES A LOS PARARRAYOS, LOS CUALES SE REALIZARÁN CON CABLE #4/0 AWG. ESTOS CHICOTES SE DEJARÁN PREVISTOS ADECUADAMENTE LARGOS Y SU CONEXIÓN SE REALIZARÁ SIN UNIONES INTERMEDIAS NI DERIVACIONES A OTROS EQUIPOS.
3. TODAS LAS ESTRUCTURAS METÁLICAS, CAVAS, SOPORTES, CIERRO, ETC., QUE ESTÉN DENTRO DEL ÁREA CUBIERTA POR LA MALLA, SE DEBERÁN CONECTAR A LA MISMA, AUN CUANDO NO SE INDIQUE EXPRESAMENTE EN LOS PLANOS.
4. LOS POSTES DE ALUMBRADO VIAL QUE ESTÁN FUERA DE LA SUPERFICIE CUBIERTA POR LA MALLA, SE PONDRÁN A TIERRA CON UN ANILLO LOCAL.
5. CUANDO LA MALLA INTERFERA CON FUNDACIONES, EL CABLE LAS DEBERÁ BORDAR.
6. LAS UNIONES ENTRE LOS EQUIPOS Y LA MALLA BASE DEBERÁN SER LO MAS CORTAS Y RECTAS POSIBLES, A PESAR DE QUE POR CLARIDAD EN EL PLANO, NO SE DIBUJEN TODOS LOS CHICOTES EN LA TRAYECTORIA MAS CORTA.
7. TANTO LOS EQUIPOS COMO SUS RESPECTIVAS ESTRUCTURAS, SE DEBERÁN CONECTAR A LA MALLA MEDIANTE DERIVACIONES INDEPENDIENTES.
8. LAS UNIONES ENTRE LA MALLA BASE Y LOS CHICOTES DE CONEXIÓN A LOS EQUIPOS Y ESTRUCTURAS SE DEBERÁN REALIZAR MEDIANTE EL SISTEMA DE TERMOFUSIÓN TIPO CADDWELD.
9. EL CIERRO METÁLICO DEL PATIO DEBERÁ SER CONECTADO A LA MALLA BASE CADA 10m APROX. CON CABLE #2/0 AWG.
10. PARA CLARIDAD DEL DIBUJO, EN ALGUNOS CASOS, LA CANTIDAD DE CHICOTES INDICADOS EN LA PLANTA SE HA SIMPLIFICADO, LA CANTIDAD REAL DE CHICOTOS HACIA LOS DIFERENTES EQUIPOS Y ESTRUCTURAS, SE MUESTRA EN LOS DETALLES RESPECTIVOS.
11. EL GALVANIZADO DE LAS ESTRUCTURAS QUE RESULTE DAÑADO DURANTE LA FUSIÓN, DEBERÁ SER REPARADO Y RECONSTITUIDO DE INMEDIATO CON GALVANIZADO EN FRÍO.
12. DURANTE LA FAENA SE DEBERÁN TOMAR PRECAUCIONES PARA QUE LOS CABLES DE LOS CHICOTES NO PERDAN EL TRENADO, SOBRE TODO EN LAS CURVAS AL PRESENTARLO Y COLOCARLO ENTRE LAS ESTRUCTURAS.
13. SE DEBERÁ RESPECTAR EL NIVEL DE ENTERRAMIENTO DEL CABLE DE MALLA A PUESTA A TIERRA A 600mm DESDE EL NIVEL DE PISO TERMINADO EN TODA SU EXTENSIÓN.
14. EL DISEÑO CONSIDERARÁ LA INSTALACIÓN DE UNA CAPA SUPERFICIAL DE 0,15 m DE GRANILLA DE UNA RESISTIVIDAD DE 5000 Ω-M PARA TODA LA MALLA. LA MISMA DEBERÁ SER CONTENIDA CON SOLLERAS DE HORMIGÓN U OTRO MEDIO EQUIVALENTE.
15. LAS PARRILLAS DE OPERADORES Y ESTRUCTURAS METÁLICAS, SE COLOCARÁN A TIERRA EN AL MENOS DOS PUNTOS.
16. LAS PANTALLAS METÁLICAS DE LOS CABLES AISLADOS DEBEN SER PUESTAS A TIERRA.

NOTAS:			REV. N° FECHA DESCRIPCIÓN			PROPIETARIO SOCIEDAD AUSTRAL DE TRANSMISIÓN TRONCAL S.A.			O.F.V. O.F.V. J.E.G. R.A.L. 08-03-2021		PROYECTO SUBESTACIÓN SECCIONADORA LA RUCA 110 KV	
						ACTIVIDAD NOMBRE FECHA					PLANO MALLA DE PUESTA A TIERRA PATIO PLANTA	
						PROYECTO IMELSA 08-03-2021						
						DIBUJO IMELSA 08-03-2021						
						REVISO SATT						
						APROBÓ SATT						
B 08-03-2021 EMITIDO PARA REVISIÓN						ESCALA 1/50			REVISIÓN		N° DE PLANO	
A 08-03-2021 EMITIDO PARA COORDINACIÓN INTERNA						PB/PROYECTO N° 100/TT-315-02			SE-315T003-P-EE-02-001-100			