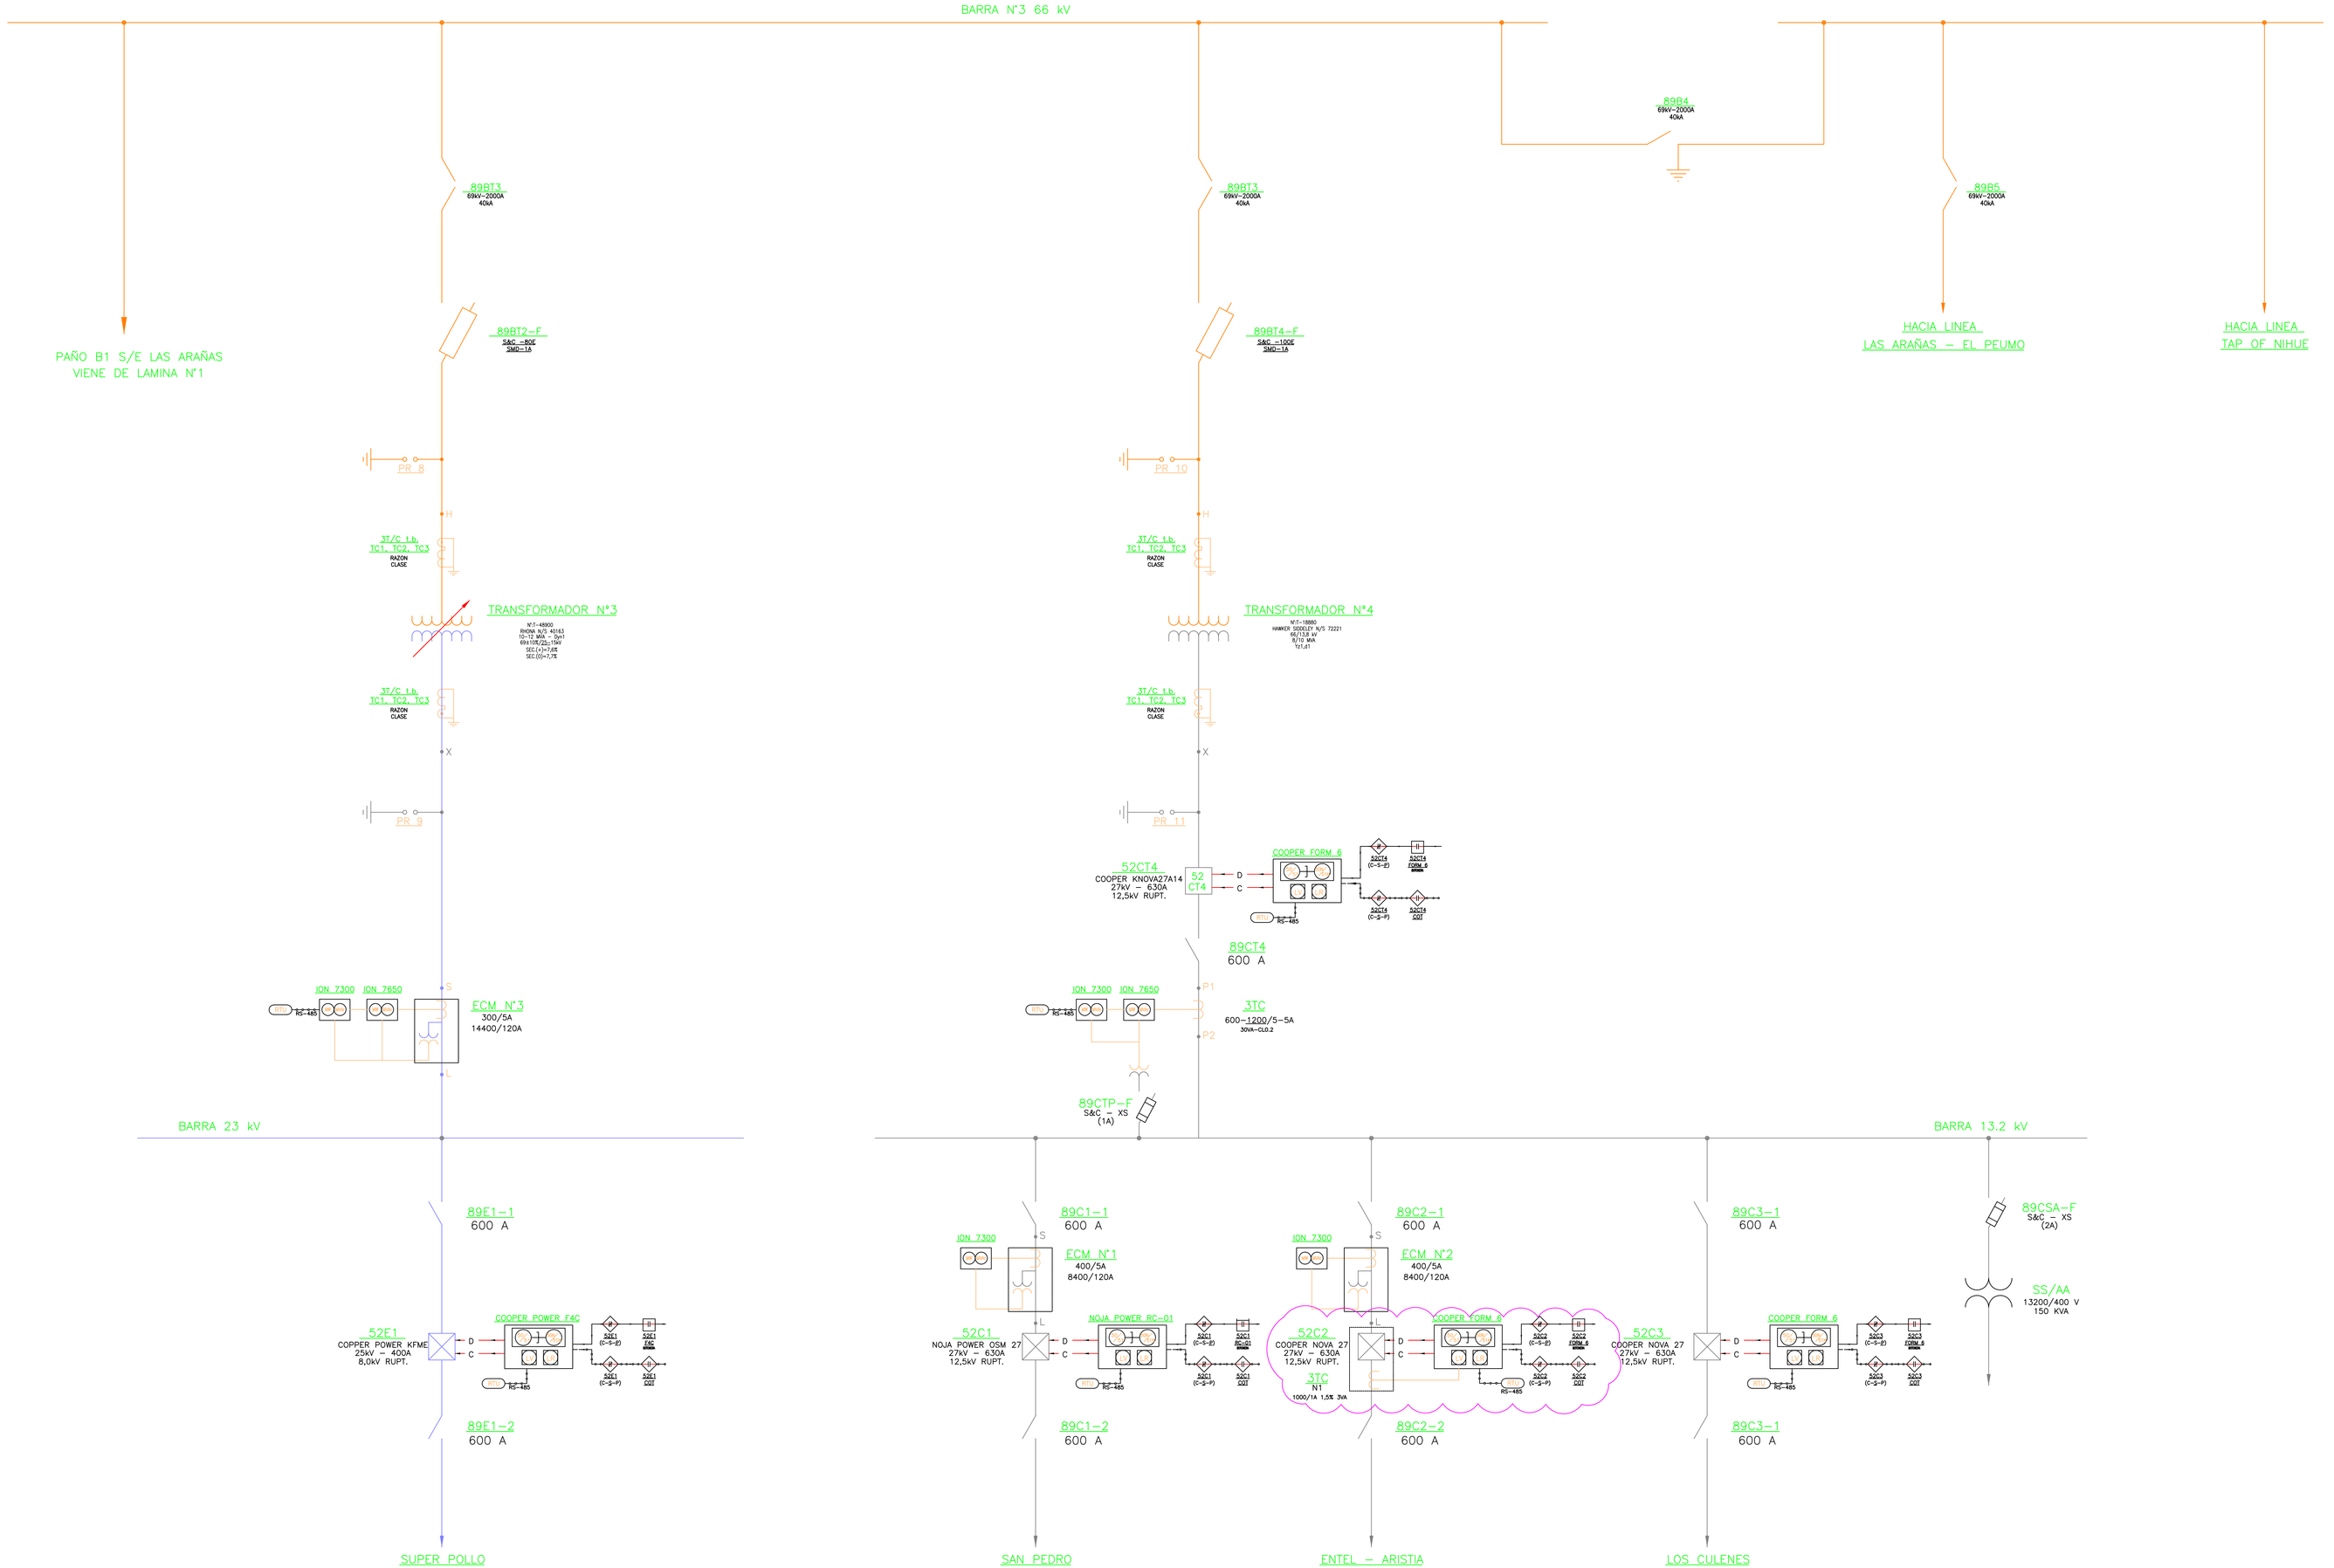


ABREVIACIONES EQUIPOS

TR	TRANSFORMADOR DE PODER
TC	TRANSFORMADOR DE CORRIENTE
TP	TRANSFORMADOR DE POTENCIAL
TSA	TRANSFORMADOR DE SERVICIOS AUXILIARES
SWC(INT)	SWITCH LOCAL CIERRE/DESENGANCHE
SWC	SWITCH REMOTO CIERRE/DESENGANCHE
63Y	RELES BAJA PRESION SF6
63	MANOSTATO BAJA PRESION SF6
SWC	SWITCH DE CONTROL DE INTERRUPTOR
33/M	SWITCH LIMITE MOTOR
43/73(L-S)	SWITCH SELECTOR LOCAL/SCADA
RR	PARARRAYOS
a	CONTACTO ABIERTO CUANDO EL MEC PPAL ESTA ABIERTO
b	CONTACTO CERRADO CUANDO EL MEC PPAL ESTA ABIERTO
F	FUSIBLE
LR	LUZ ROJA
LV	LUZ VERDE
F6	UNIDAD DE CONTROL DIGITAL TIPO FORM 6
TM	INTERRUPTOR TERMOMAGNETICO
TDCA	TABLERO DISTRIBUCION DE CORRIENTE ALTERNA
CA	CARGADOR BATERIA
L-R	SWITCH SELECTOR LOCAL-REMOTO
MP	MODULO PROGRAMACION RECONECTADOR FSC
MF	MEDIDOR MULTIFUNCION PROGRAMABLE PML 7300 ION

- INSTRUMENTO DE CAMPO SIN INDICACIÓN TERRENO
- INSTRUMENTO DE CAMPO CON INDICACIÓN EN TERRENO
- INSTRUMENTO CON INDICACIÓN EN TABLERO Y PC
- INSTRUMENTO CON INDICACIÓN EN TERRENO, TABLERO Y PC
- INSTRUMENTO CON INDICACIÓN SOLO EN PC
- INSTRUMENTO CON INDICACIÓN EN TERRENO Y PC
- COMANDO DADO DESDE RELE: NIVEL 1
- COMANDO DADO DESDE PC: NIVEL 2

- COMUNICACIÓN POR SOFTWARE
- COMUNICACIÓN INTERNA DEL RELÉ O RTU

NUMEROS NEMA

26	INDICADOR DE TEMPERATURA
30	CUADRO ANUNCIADOR DE ALARMAS
26T	TEMPERATURA DE ENROLLADOS
51	RELE SOBRECORRIENTE DE FASES TEMPORIZADO
51N	RELE SOBRECORRIENTE RESIDUAL TEMPORIZADO
52	INTERRUPTOR DE POTENCIA
24	INDICADOR DE NIVEL
R6	RELE MAESTRO
87	RELE DIFERENCIAL
89	SECCIONADOR

SUFIJOS

B	EQUIPO EN 66kV
C	EQUIPO EN 13,2kV
Q	ACEITE
L	LOCAL
R	REMOTO
T	TELECONTROL
MR	MULTIRELACION
F	VENTILADOR
X	RELE AUXILIAR

REFERENCIAS

23838-A1 DIAGRAMA ELEMENTAL DE CORRIENTE ALTERNA
23864-A1 DIAGRAMA ELEMENTAL DE CORRIENTE CONTINUA
23837-A1 DIAGRAMA ALAMBRADO TABLERO
23836-A1 DIAGRAMA ALAMBRADO REMOTO VARIOS

N°	PROYECTOS	PROY.	APROBO	FECHA

TRANSNET GRUPO CGE

ZONA
MELIPILLA

SUBESTACIÓN LAS ARAÑAS 110/66/13,8 kV

DIAGRAMA UNILINEAL Y FUNCIONAL

REVISO	D.M.G.	DIBUJO	D.M.G.	PLANO N°	23834-A0
APROBO	D.M.G.	PROYECTO	D.M.G.		
FECHA	11-2019	ESCALA	NO	HOJA N°	06 SIGUE EN